

PROYECTO

Habitaculo Palta Airbnb.

This architectural section drawing illustrates the cross-section of a curved house. The drawing shows various rooms including a Kitchen (COCINA), a Bath (BAÑO), a Shower (DUCHA), and a Dining Room (COMEDOR). External features include a window (VENTANA), structural limits (LIMITE ESTRUCTURA), and finished exterior walls (LIMITE FACHADA TERMINADA EXTERIOR). The drawing is labeled with sections A-A', B-B', C-C', and D-D'.

PROYECCION ESTRUCTURA ANTEPECHO

VENTANA

LIMITE ESTRUCTURA

LIMITE FACHADA TERMINADA EXTERIOR

A'

B'

C'

D'

D

C

B

A

ESTAR

COCINA

BAÑO

DUCHA

COMEDOR

342 78.2 302.8 546.7 546.8 165 80.9 103 103 37 0.6

30° 30° 30° 30° 30° 30° 30° 30° 45° 20°

SIMBOLOGIA

| | |
|---|-------------|
| △ | PR |
| ● | ARBOL |
| — | BORDE TALUD |
| — | PIE TALUD |

CUADRO DE PRS


| PR | COORDENADAS | | |
|-----|-------------|------------|--------|
| | ESTE | NORTE | COTA |
| PR1 | 294834.85 | 6344303.36 | 423.05 |
| PR2 | 294817.98 | 6344334.32 | 413.61 |

CAMILO ACCESO


PLANTA EMPLAZAMIENTO
esc. 1:200

PLANTA PRINCIPAL
esc. 1:50

1 : 50 ARQ_01

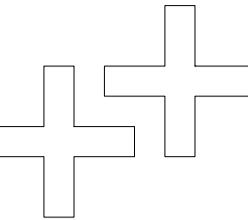



PROYECTO

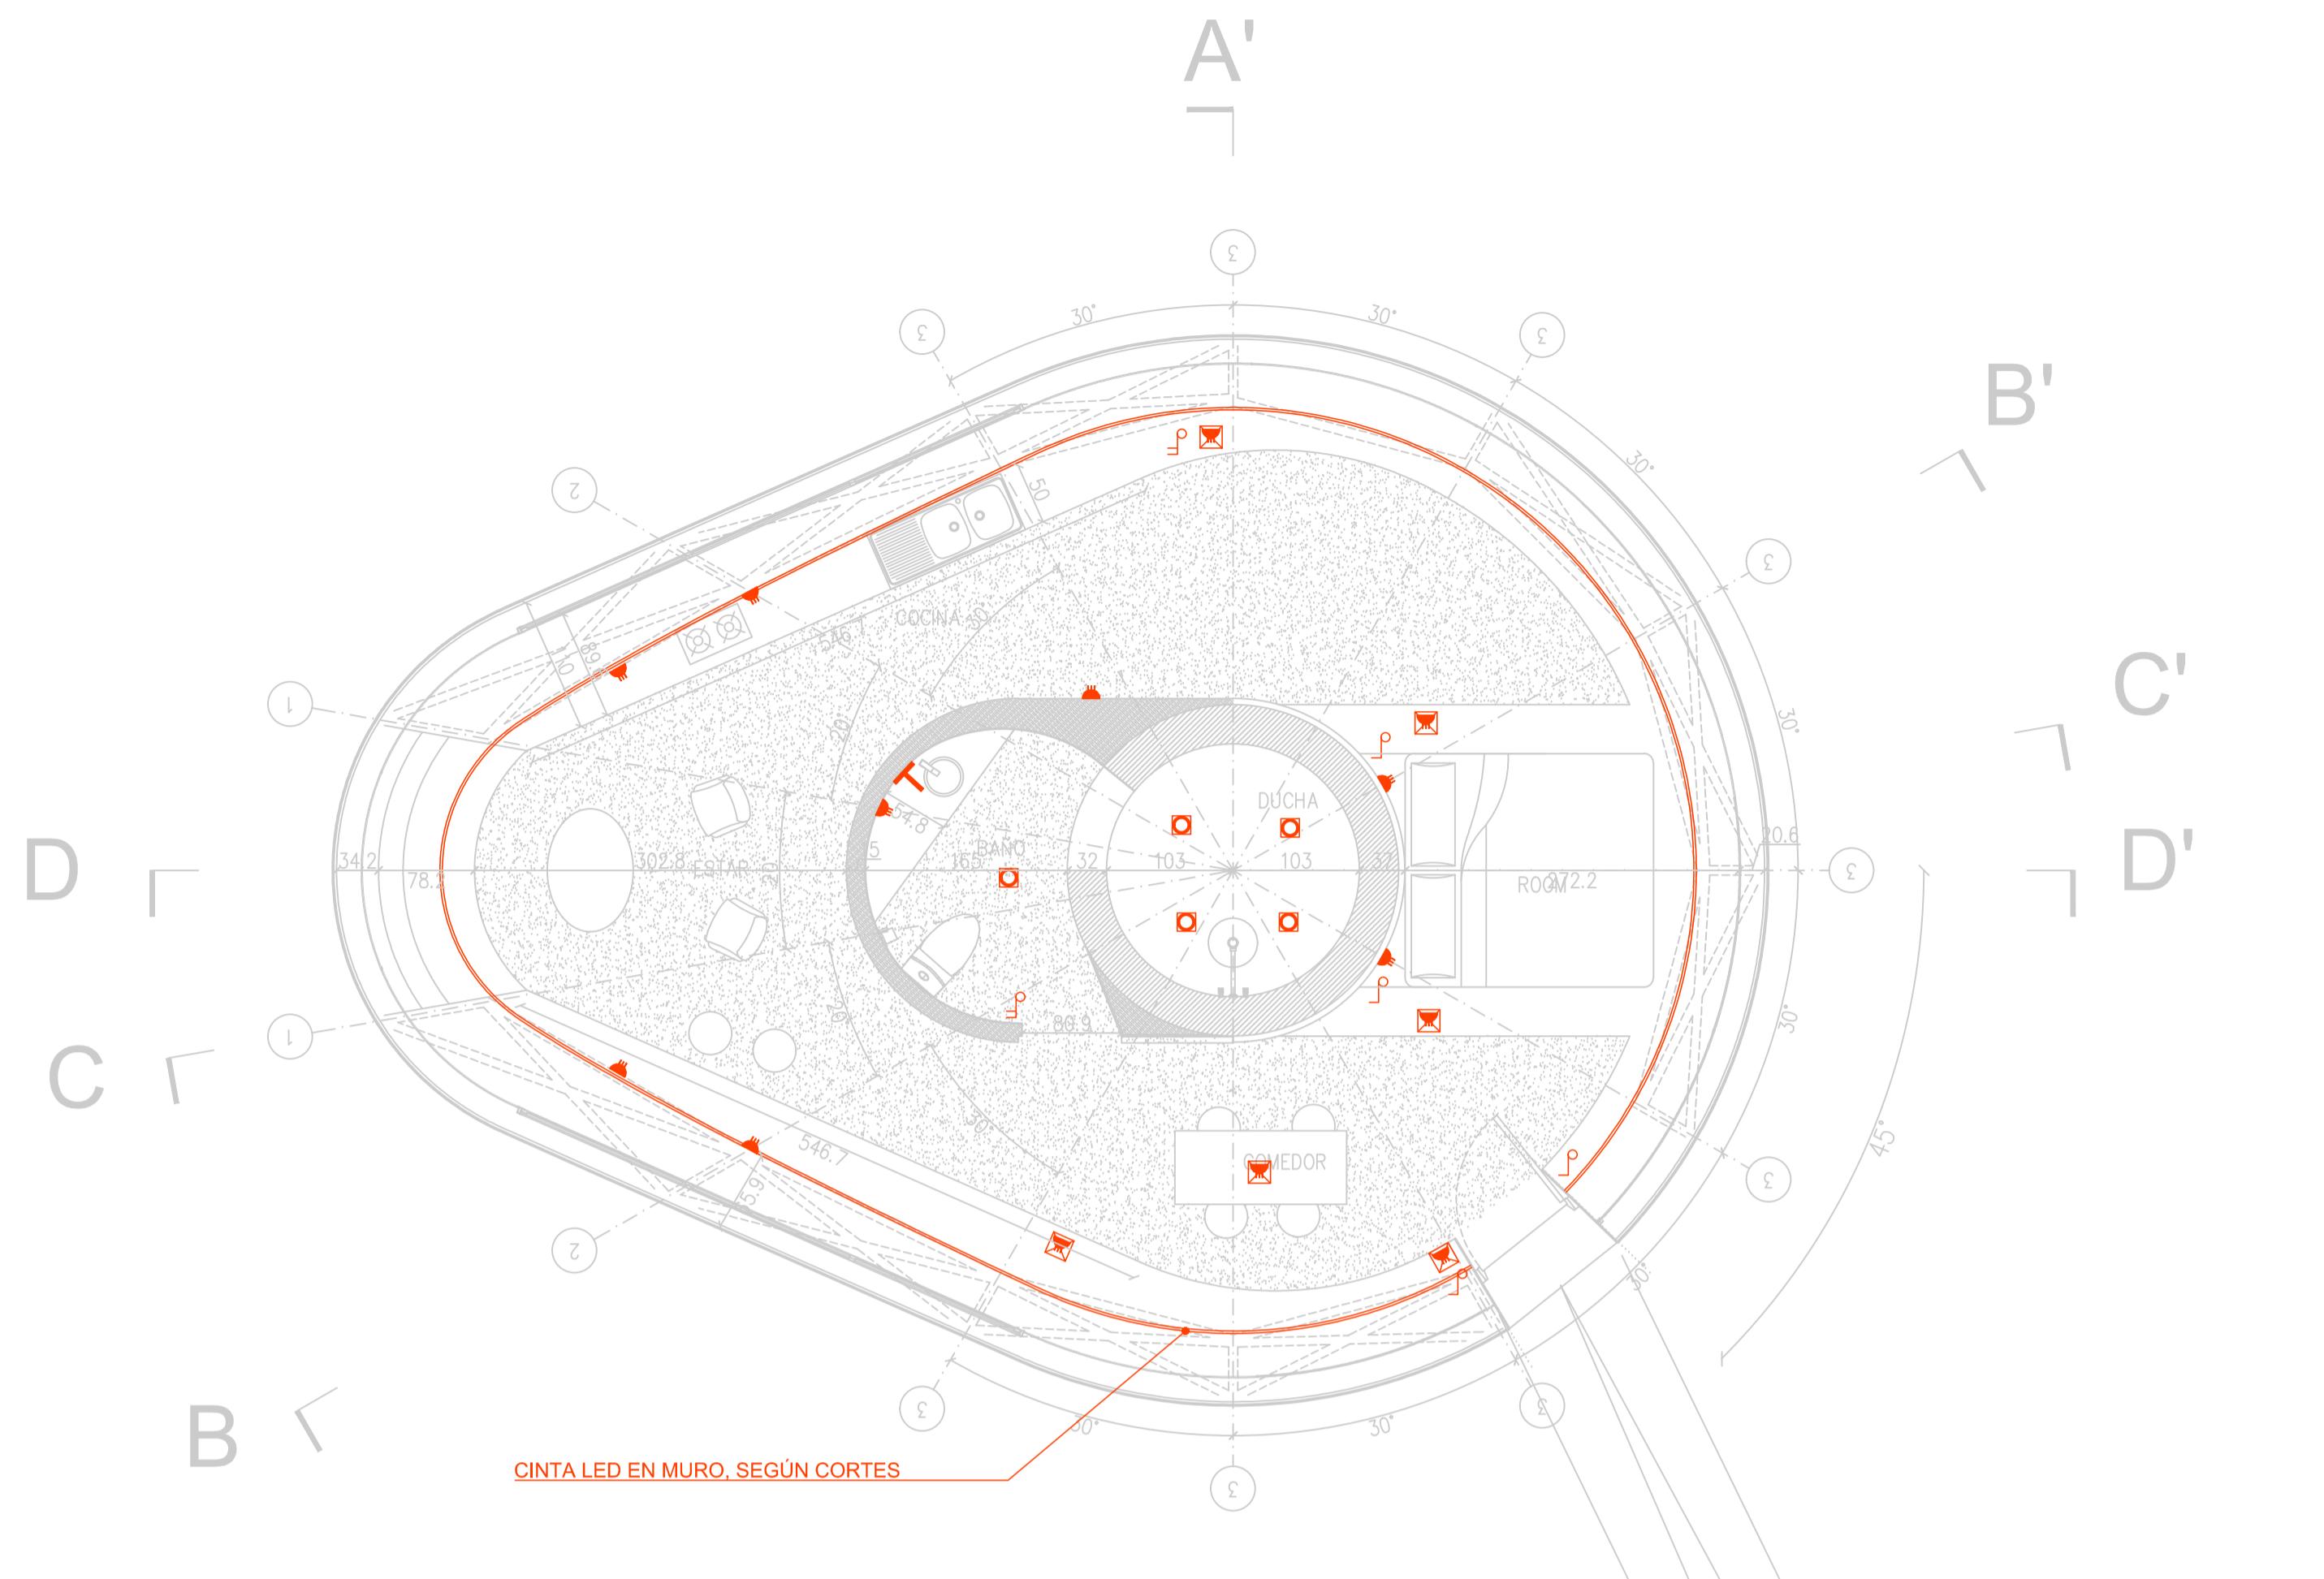**Habitaculo
Palta Airbnb.**


| | | |
|----|--|--------------|
| 3 | equipo colgante interior | cielo |
| 43 | equipo embutido interior | cielo |
| 23 | foco embutido exterior | cielo |
| 5 | foco embutido exterior | piso |
| 2 | cinta LED | mueble |
| 2 | cinta LED a 2.4 mts de altura | muro |
| 6 | dicroico dirigido | cielo |
| 3 | aplique exterior alto | muro |
| 26 | aplique exterior bajo | muro |
| 3 | aplique exterior bajo embutido para agua | muro piscina |
| 8 | dicroico dirigido | plafon |

| | | |
|----|-------------------------|------|
| 11 | interruptor simple | muro |
| 8 | interruptor simple 9/24 | muro |
| 3 | interruptor doble | muro |
| 14 | interruptor doble 9/24 | muro |
| 3 | interruptor triple | muro |
| 0 | interruptor triple 9/24 | muro |
| 1 | dimmer | muro |

| | | |
|----|------------------------------------|-----------|
| 0 | enchufe doble interior | muro |
| 36 | enchufe triple interior | muro |
| 10 | enchufe triple interior, 1m altura | muro |
| 13 | enchufe triple exterior | muro |
| 3 | enchufe triple piso | piso |
| 1 | enchufe triple piso exterior | piso |
| 1 | enchufe triple aereo | muro alto |
| 1 | enchufe triple a mueble | mueble |
| 7 | toma de TV cable | muro |
| 3 | citofono | muro |

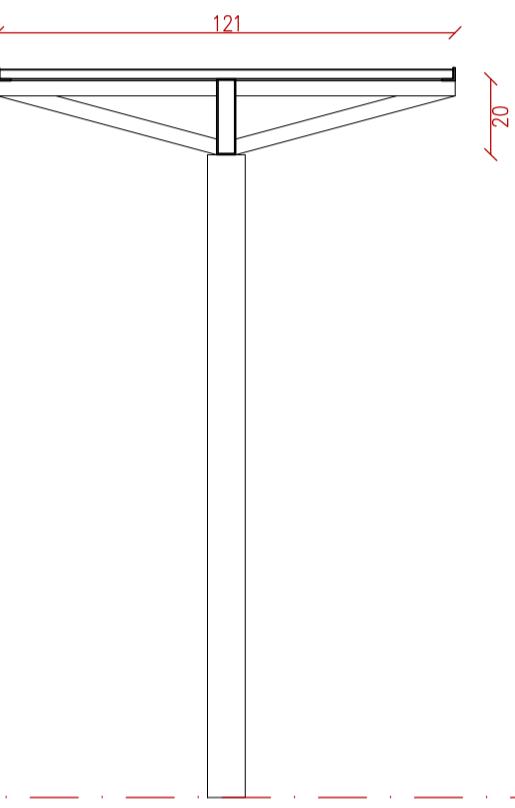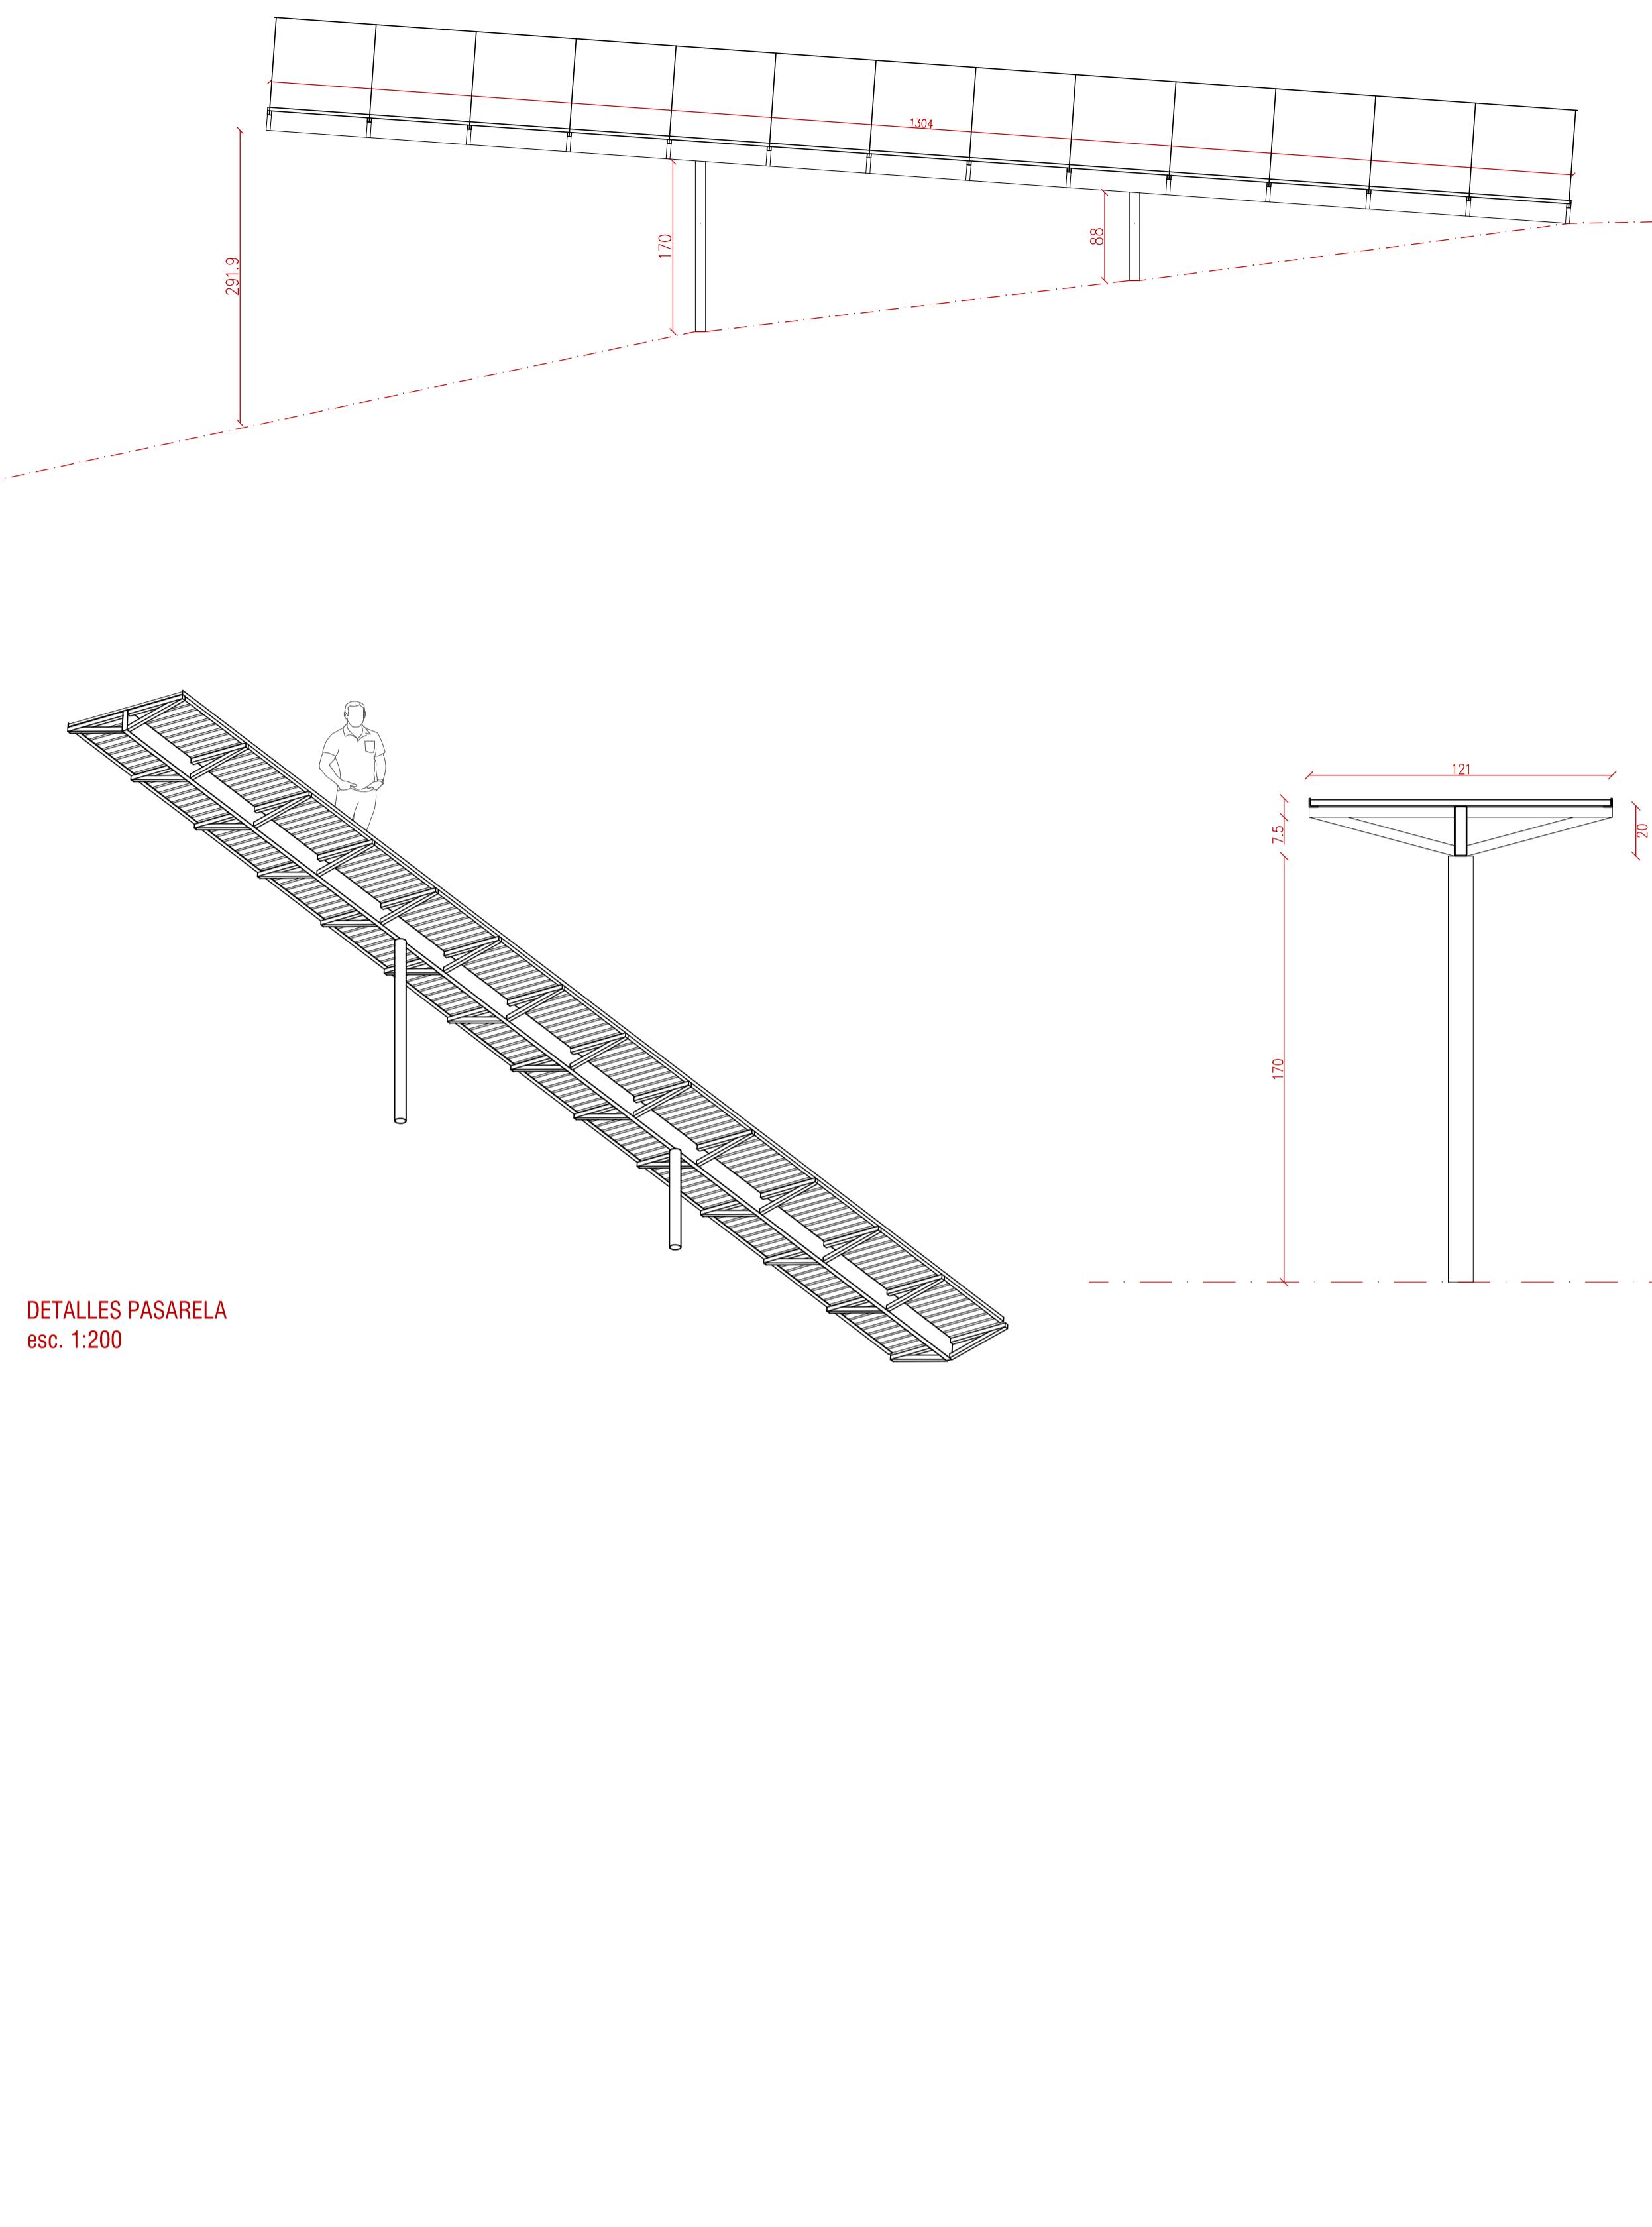PLANTA ELECTRICA
esc. 1:200


NOTAS

EDICIÓN

Entrega 01 Airbnb

MANDANTE

Ignacio Rios Michelsen
Rut:

ARQUITECTOS

MAS ES MAS
ArquitectosLucas Cerdá Ramoneda
19.078.130-5Gábor Oyarzún Casasus
16.742.060-1

DIBUJO

MAS ES MAS
Arquitectos

UBICACIÓN

Comuna de Hijuelas
Provincia de Quillota
Región de Valparaíso, Chile

Orientación




FECHA



2023 - 01 - 12

ESCALA

LÁMINA
1 : 50 ARQ_02

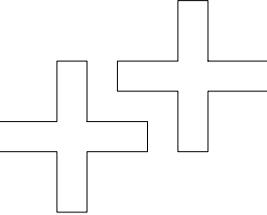

PROYECTO

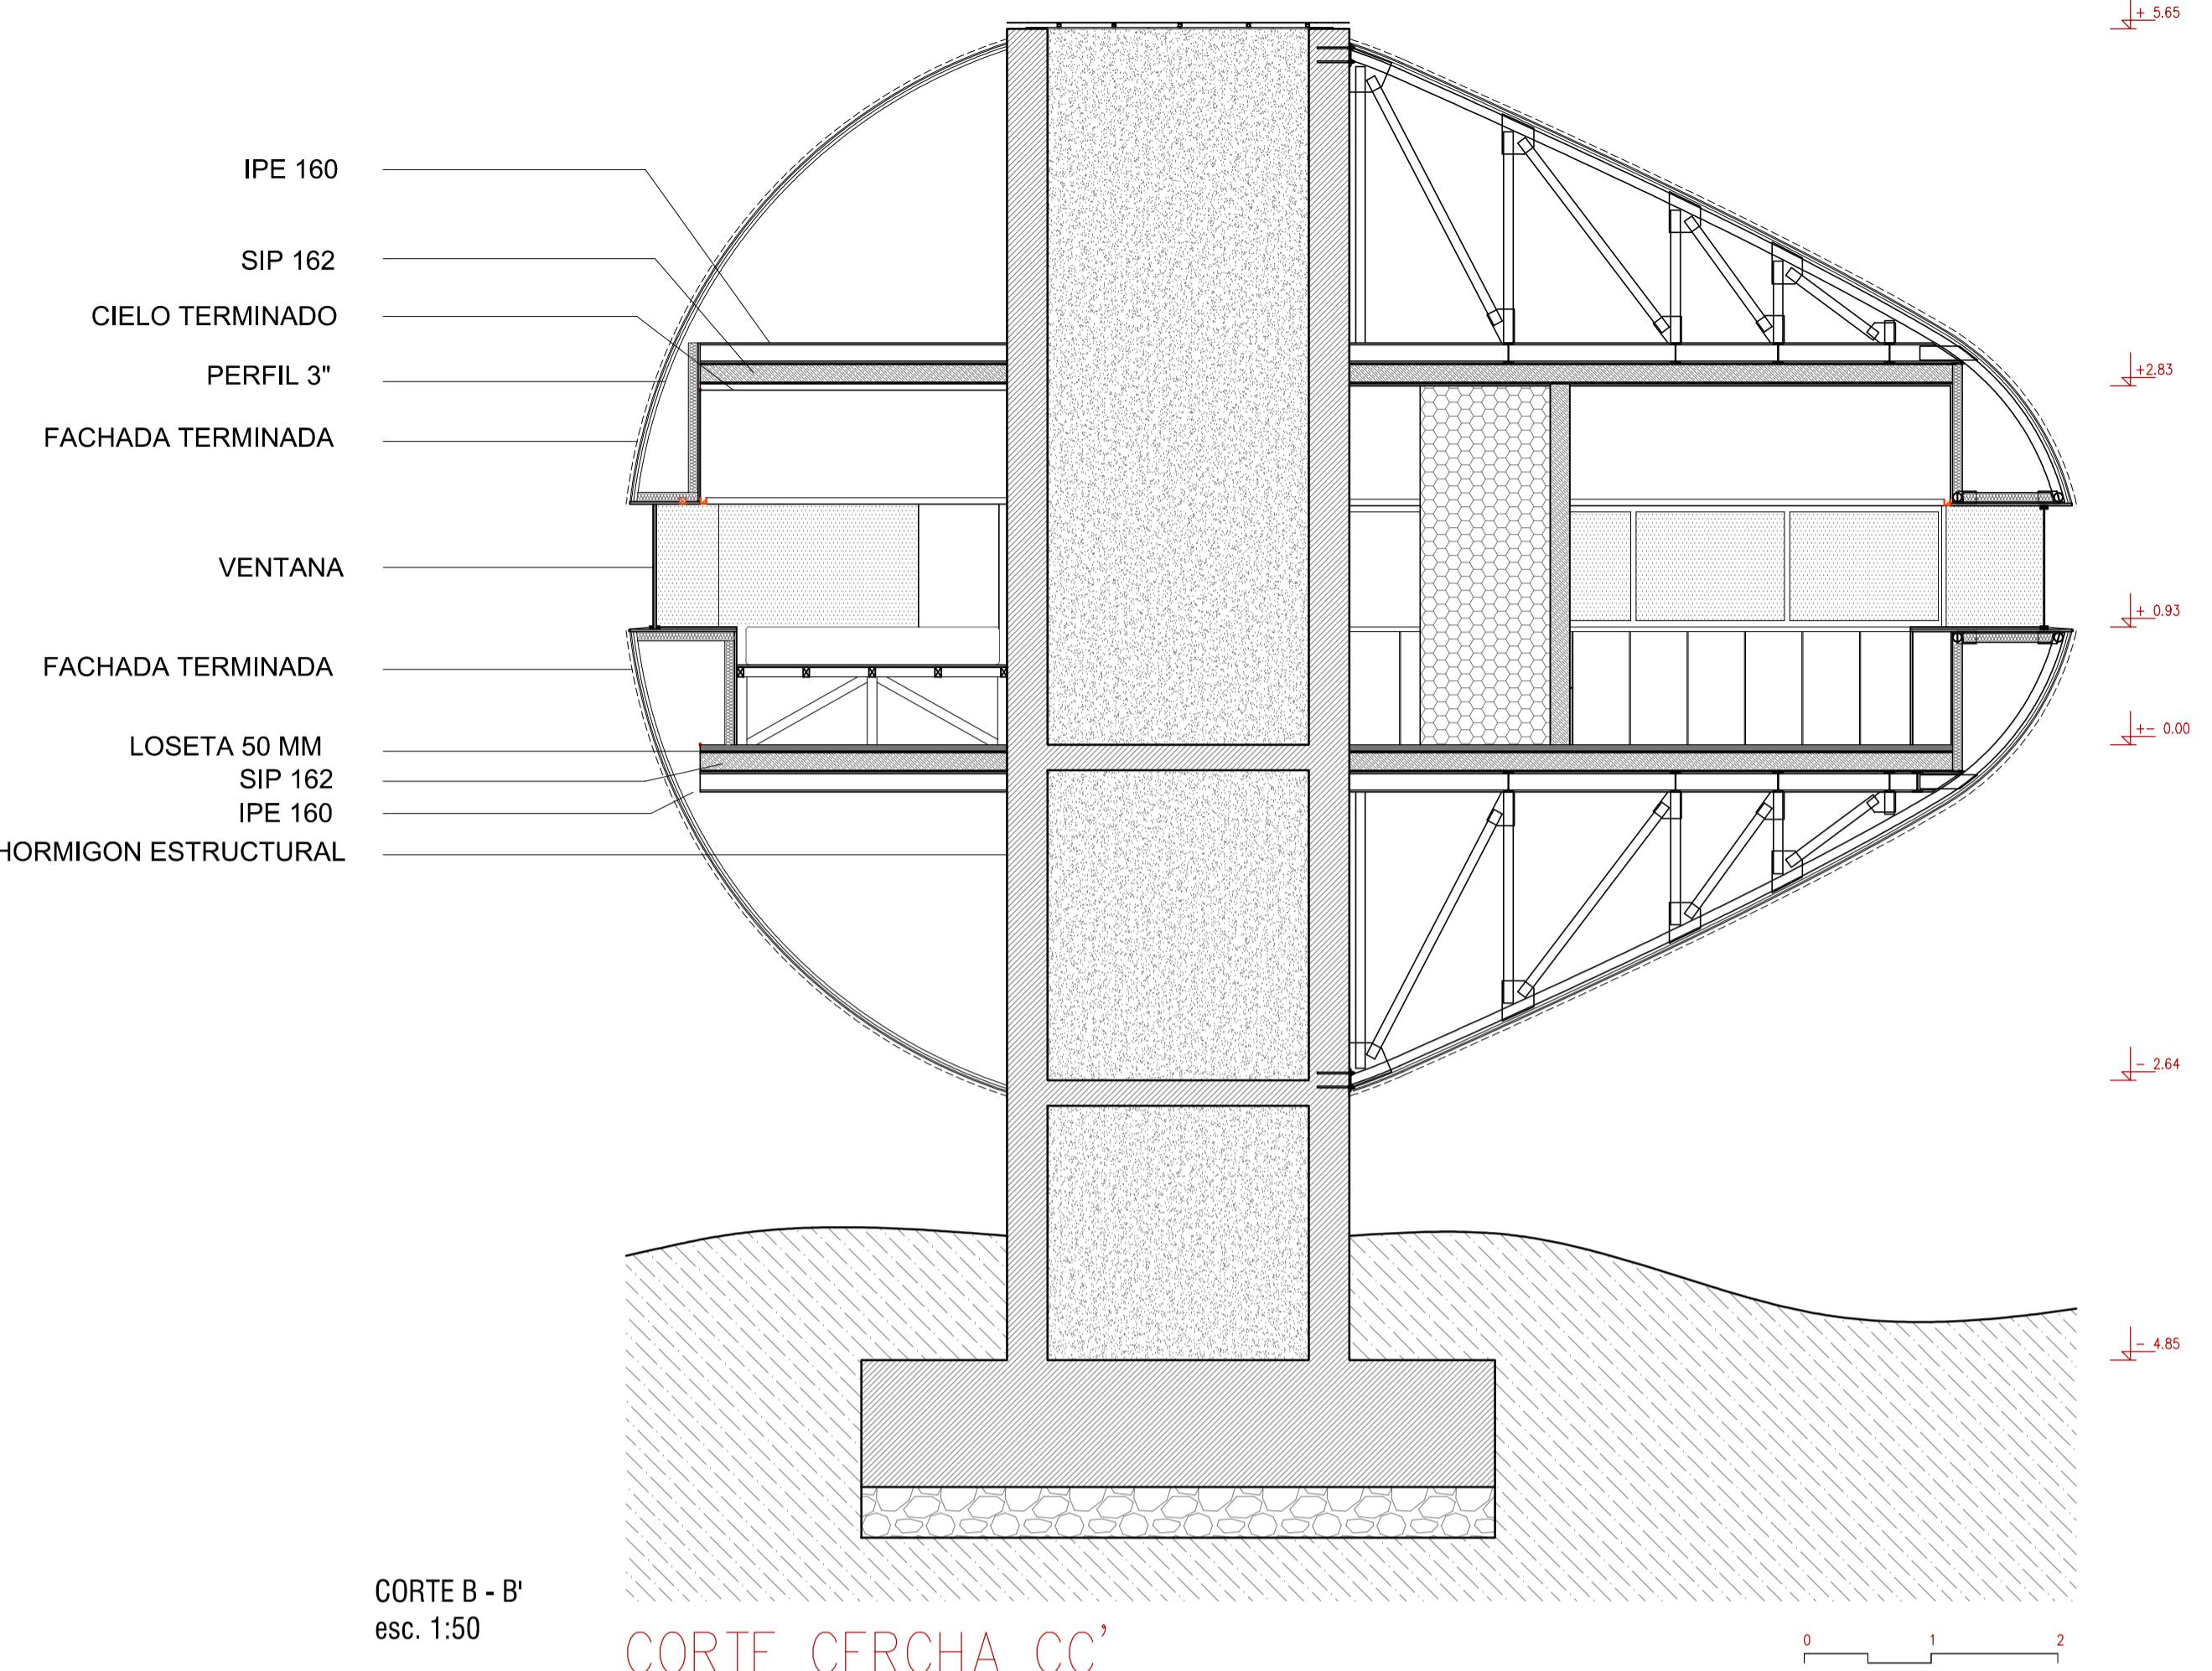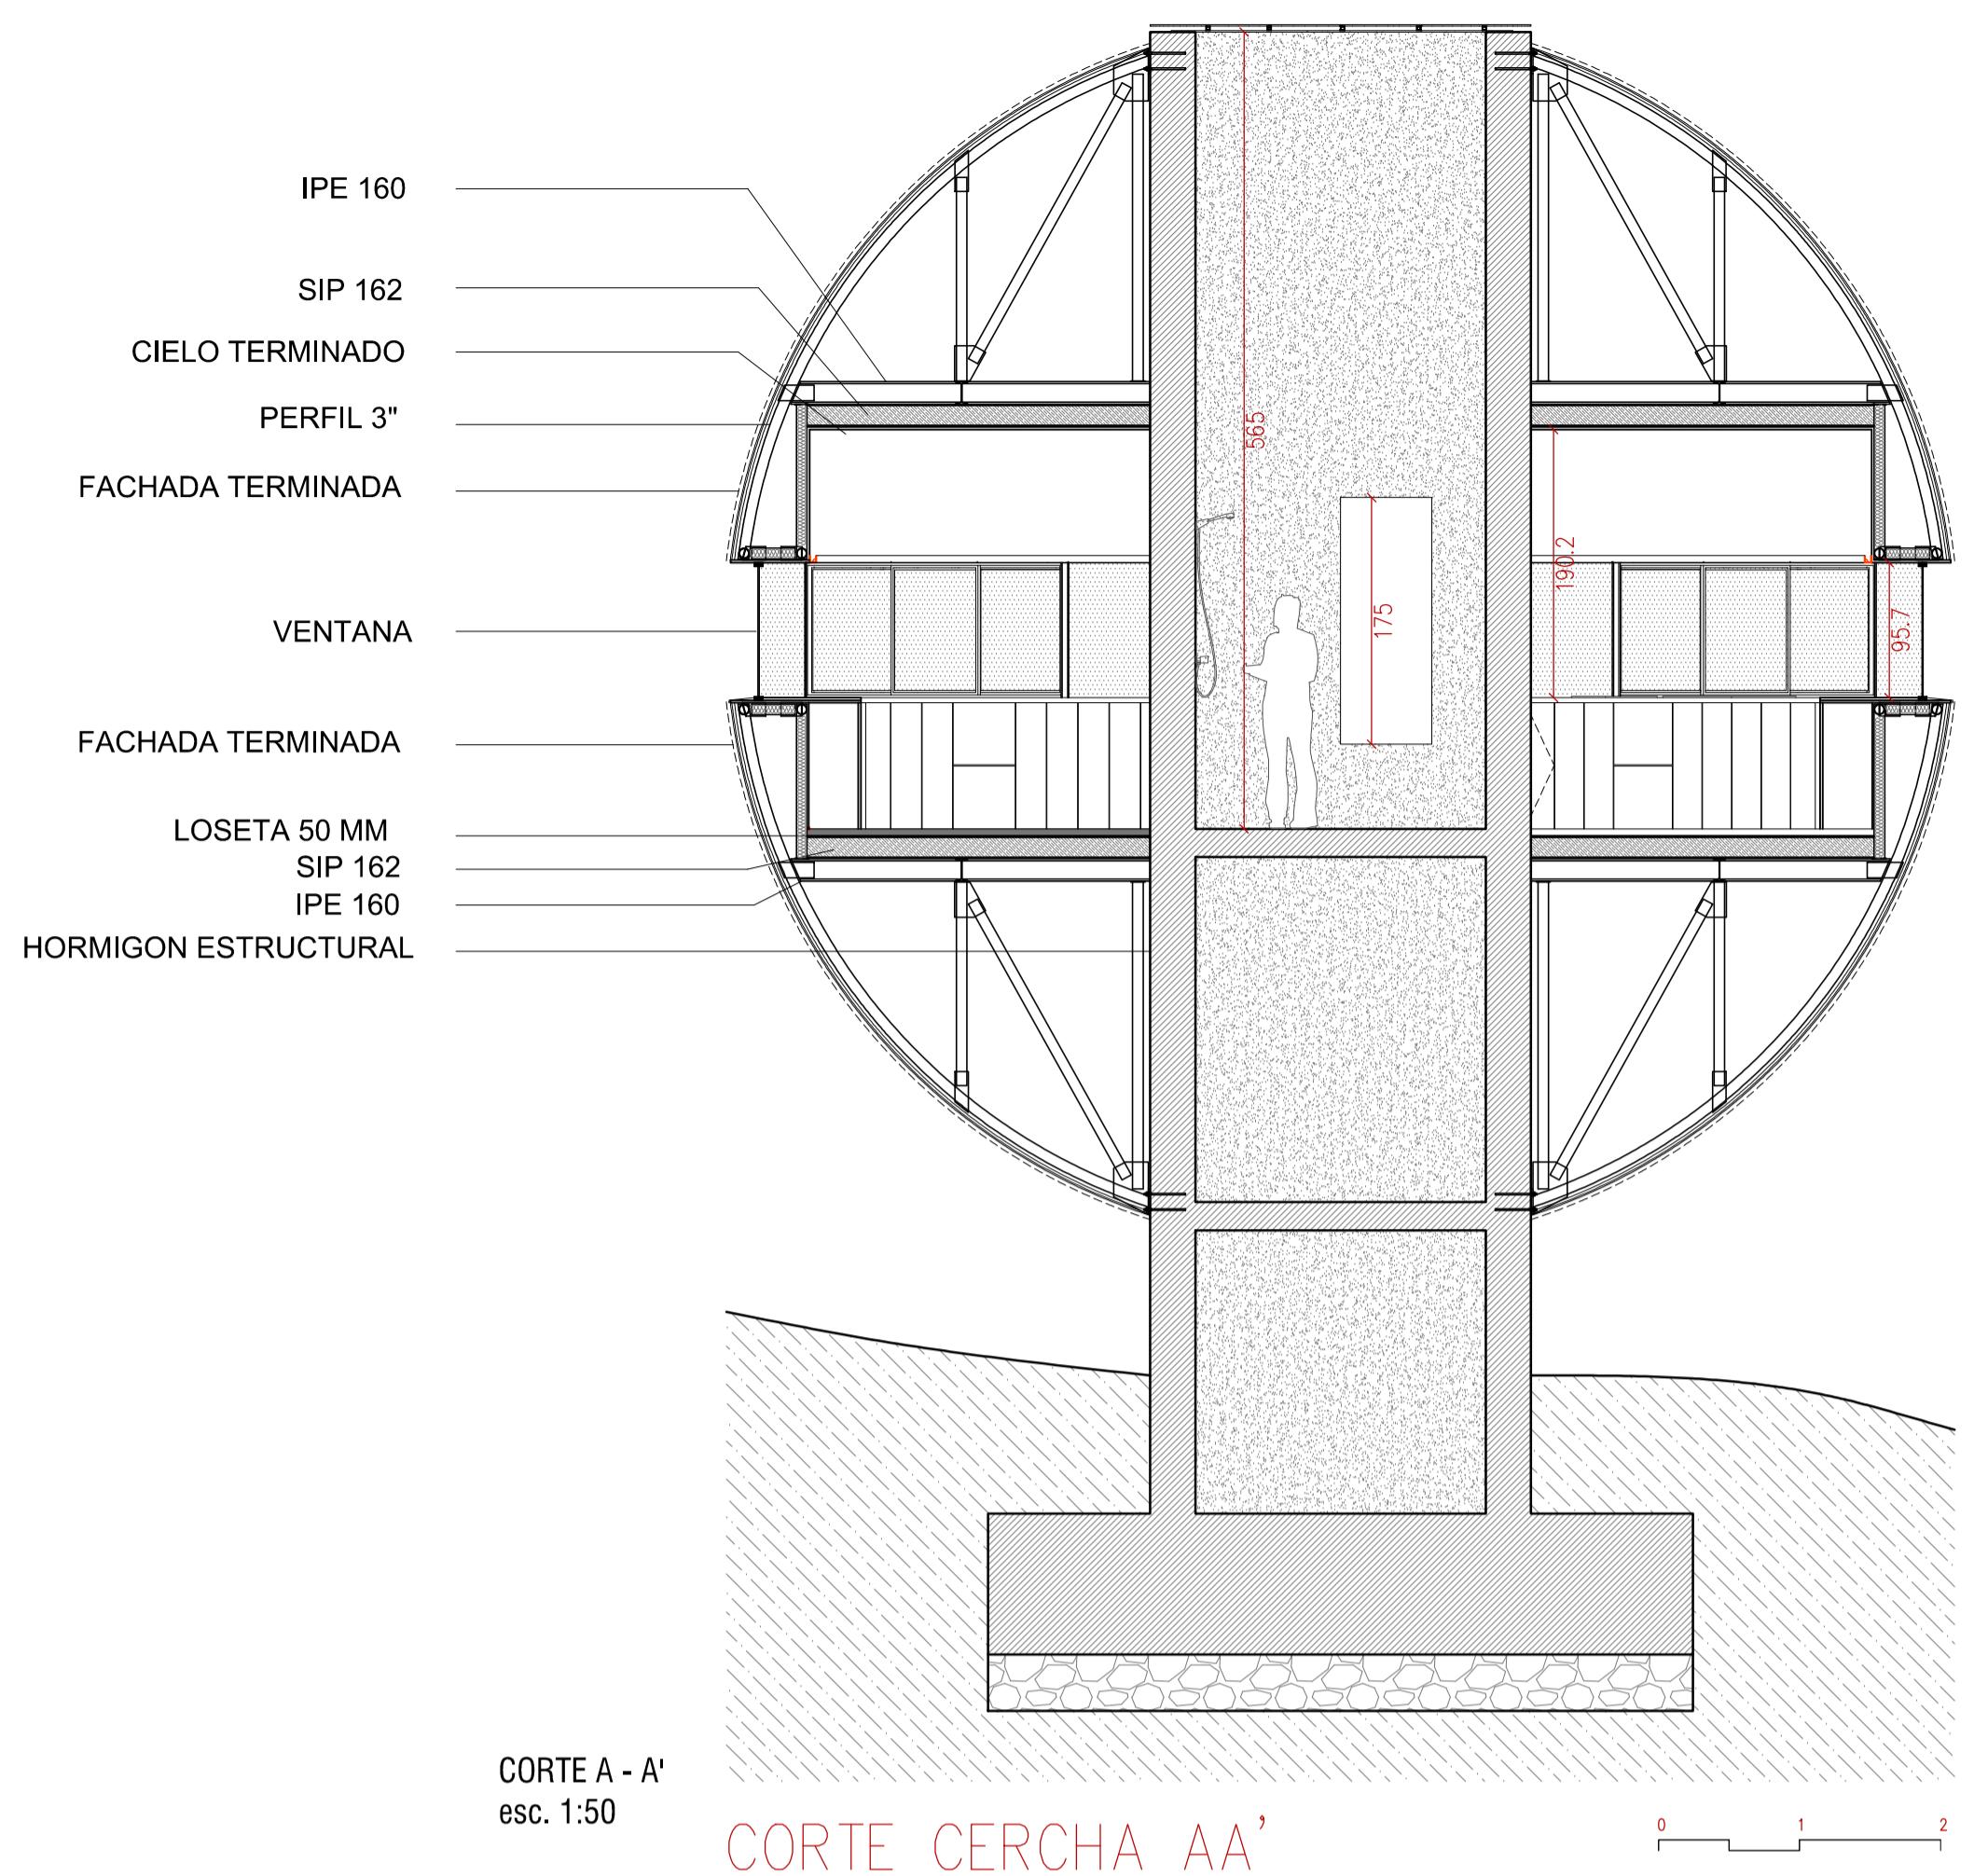**Habitaculo
Palta Airbnb.**

NOTAS

EDICIÓN

Entrega 01 Airbnb

MANDANTE

Ignacio Rios Michelsen

Rut:

ARQUITECTOS

MAS ES MAS

Arquitectos

Lucas Cerdá Ramoneda

19.078.130-5

Gabriel Oyarzún Casasus

16.742.060-1

DIBUJO

MAS ES MAS

Arquitectos

UBICACIÓN

Comuna de Hijuelas

Provincia de Quillota

Región de Valparaíso, Chile

Orientación



FECHA



2023 - 01 - 12


ESCALA



LÁMINA ARQ_03

1 : 50

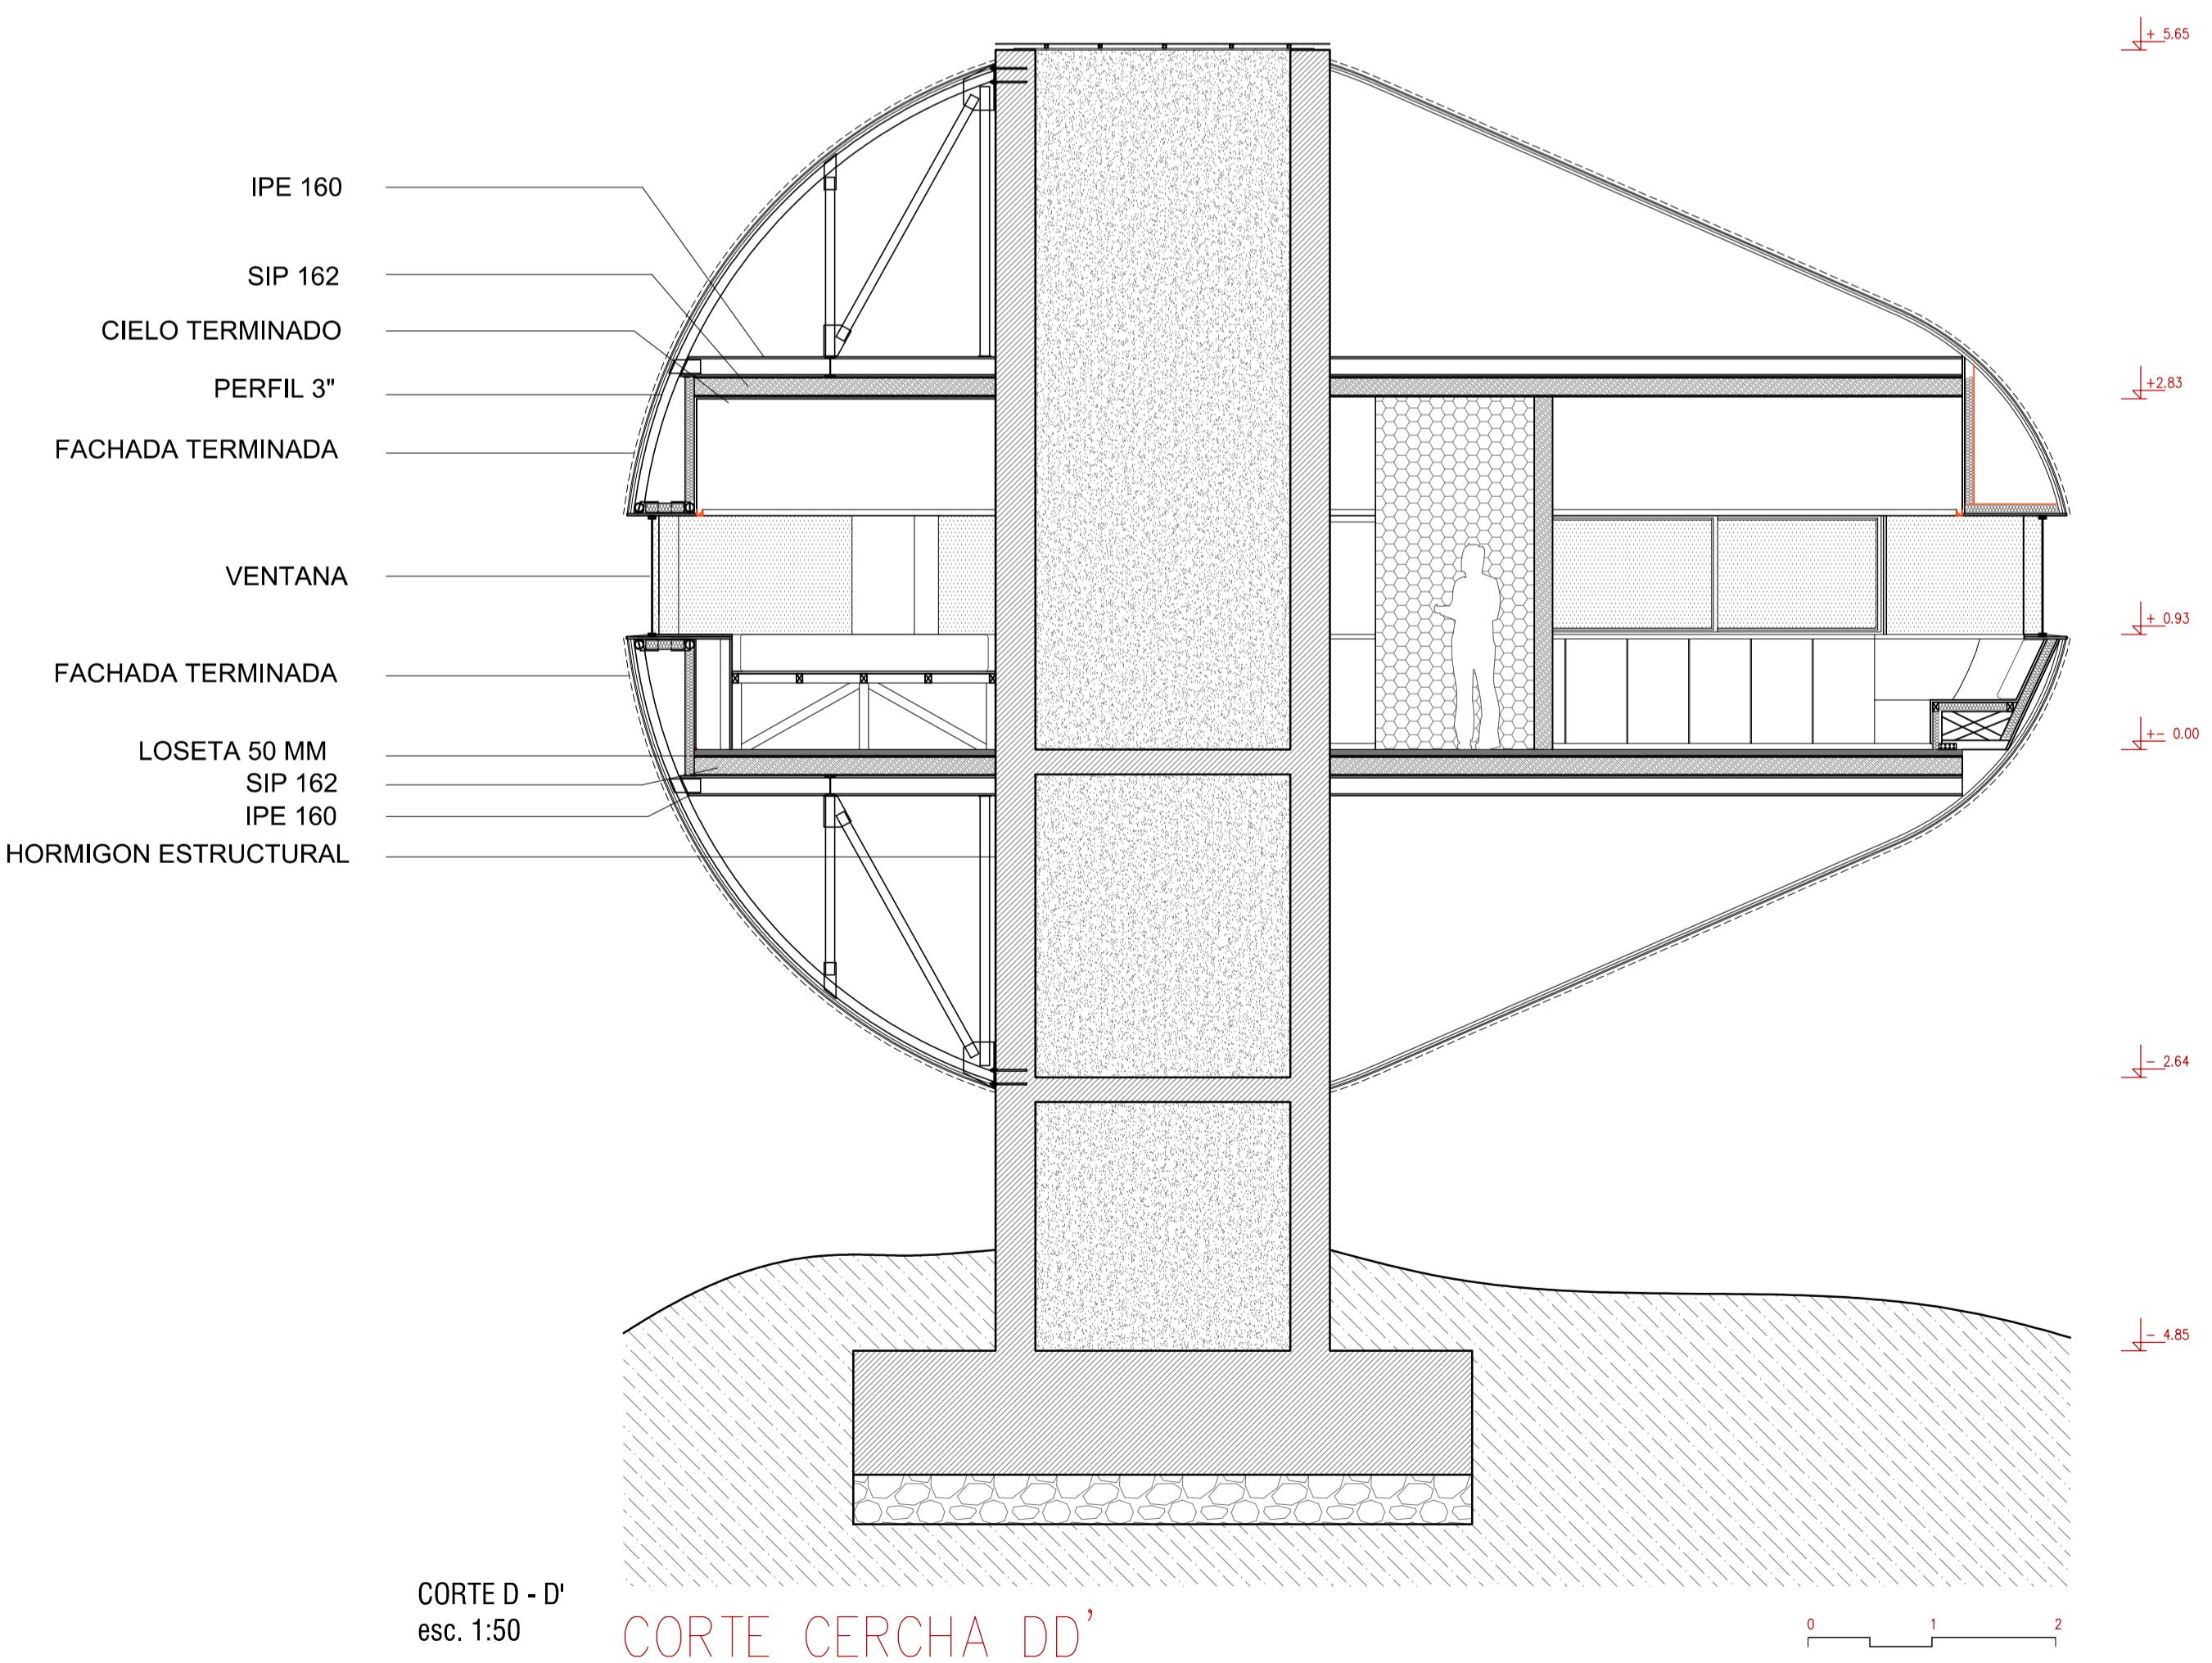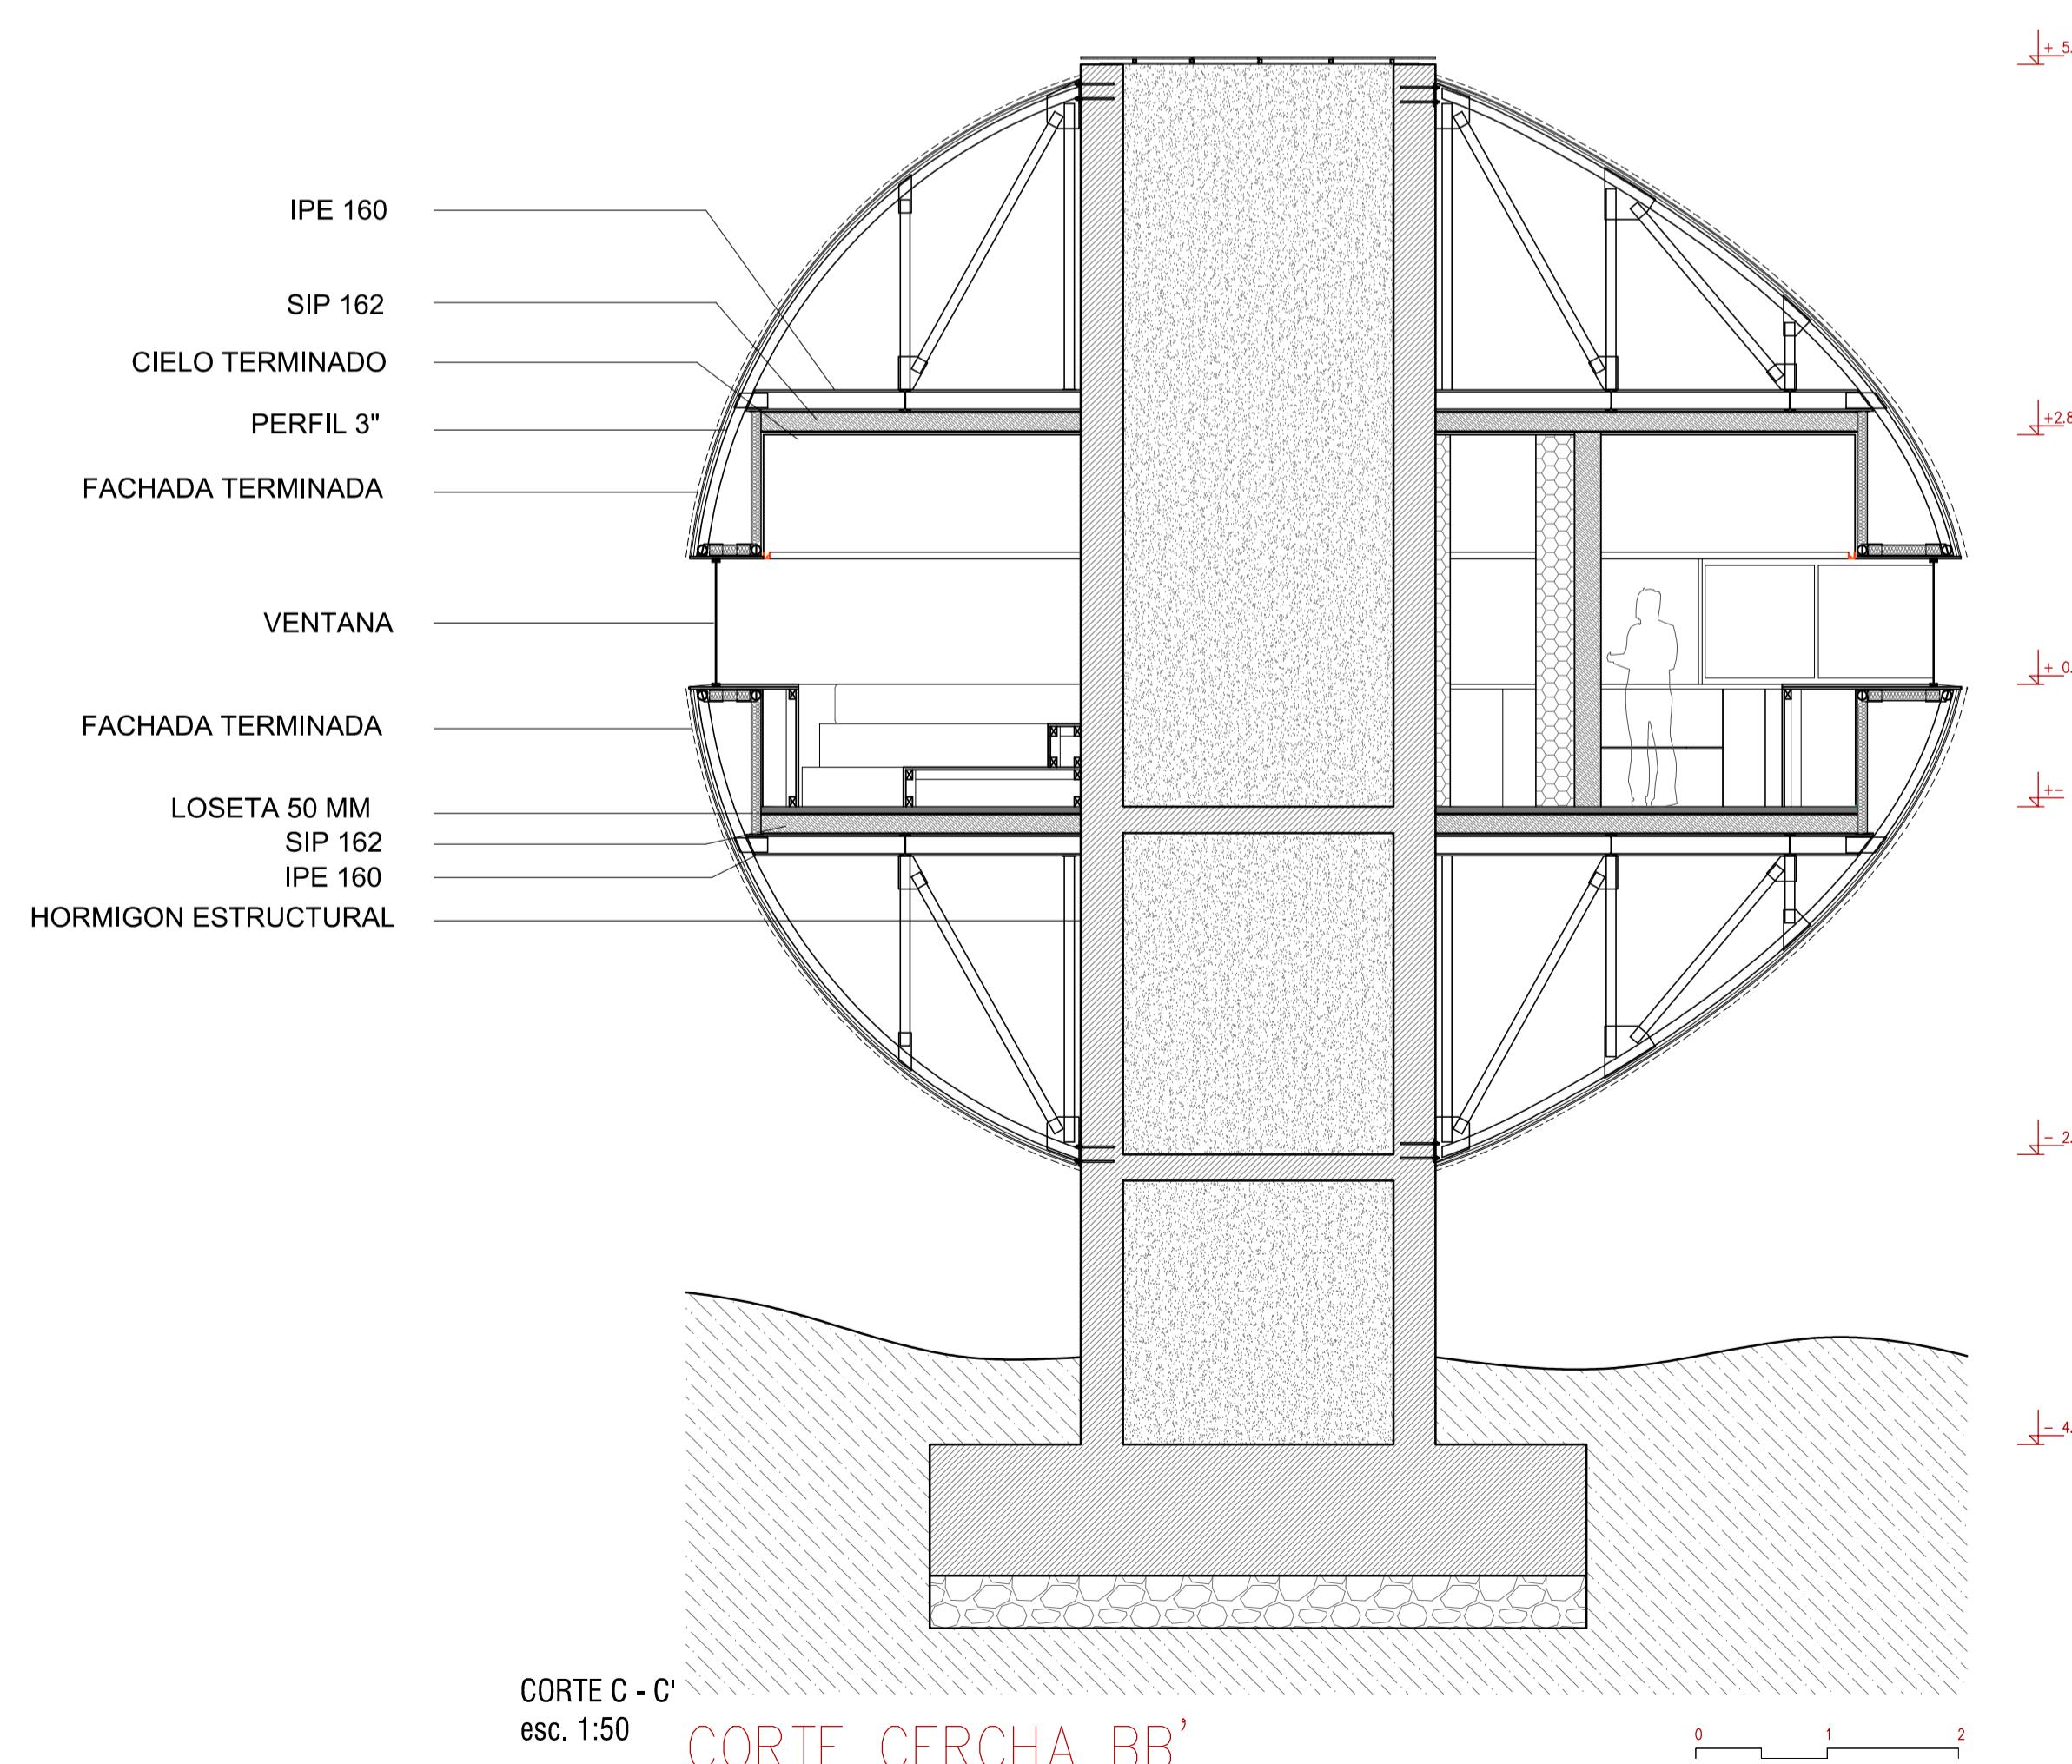

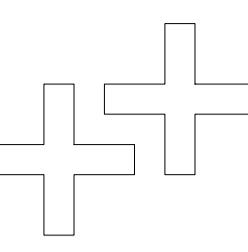

PROYECTO

**Habitaculo
Palta Airbnb.**

NOTAS

EDICIÓN

Entrega 01 Airbnb

MANDANTE

Ignacio Ríos Michelsen
Rut:

ARQUITECTOS

MAS ES MAS
Arquitectos
Lucas Cerdá Ramoneda
19.078.130-5
Gabriel Oyarzún Casasus
16.742.060-1

DIBUJO

MAS ES MAS
Arquitectos

UBICACIÓN

Comuna de Hijuelas
Provincia de Quillota
Región de Valparaíso, Chile

Orientación



FECHA


2023 - 01 - 12

ESCALA


LÁMINA

1 : 50


ARQ_04

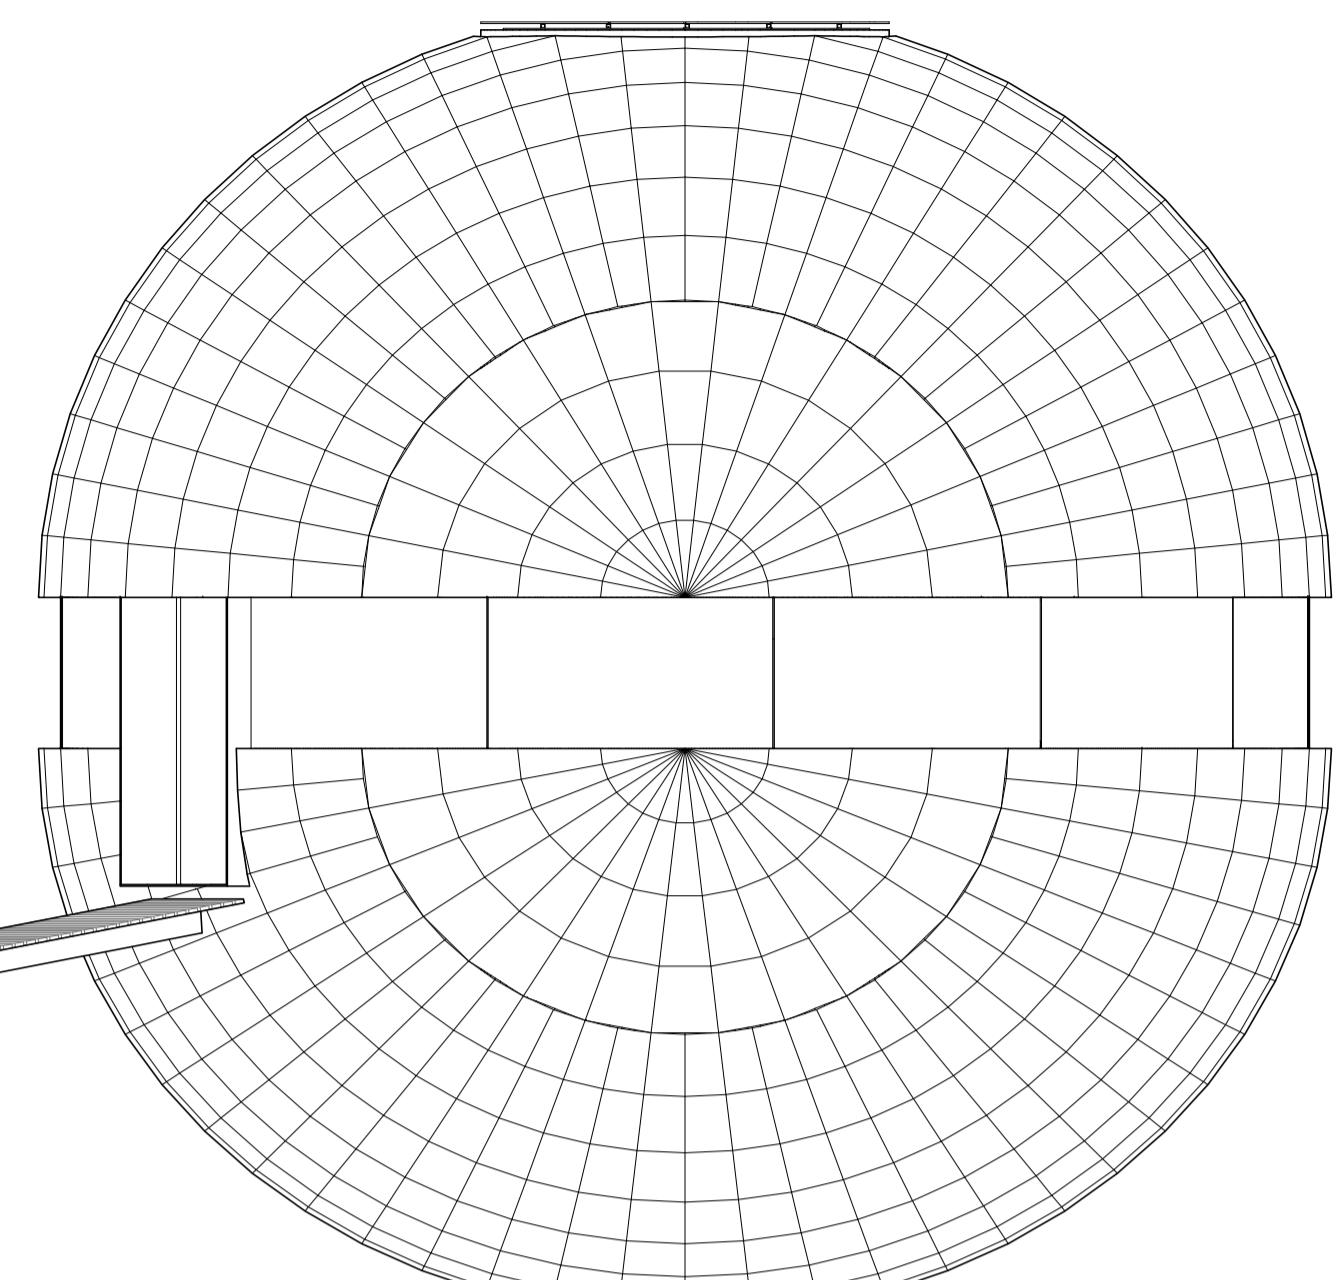


ELEVACIÓN ORIENTE
esc. 1:50

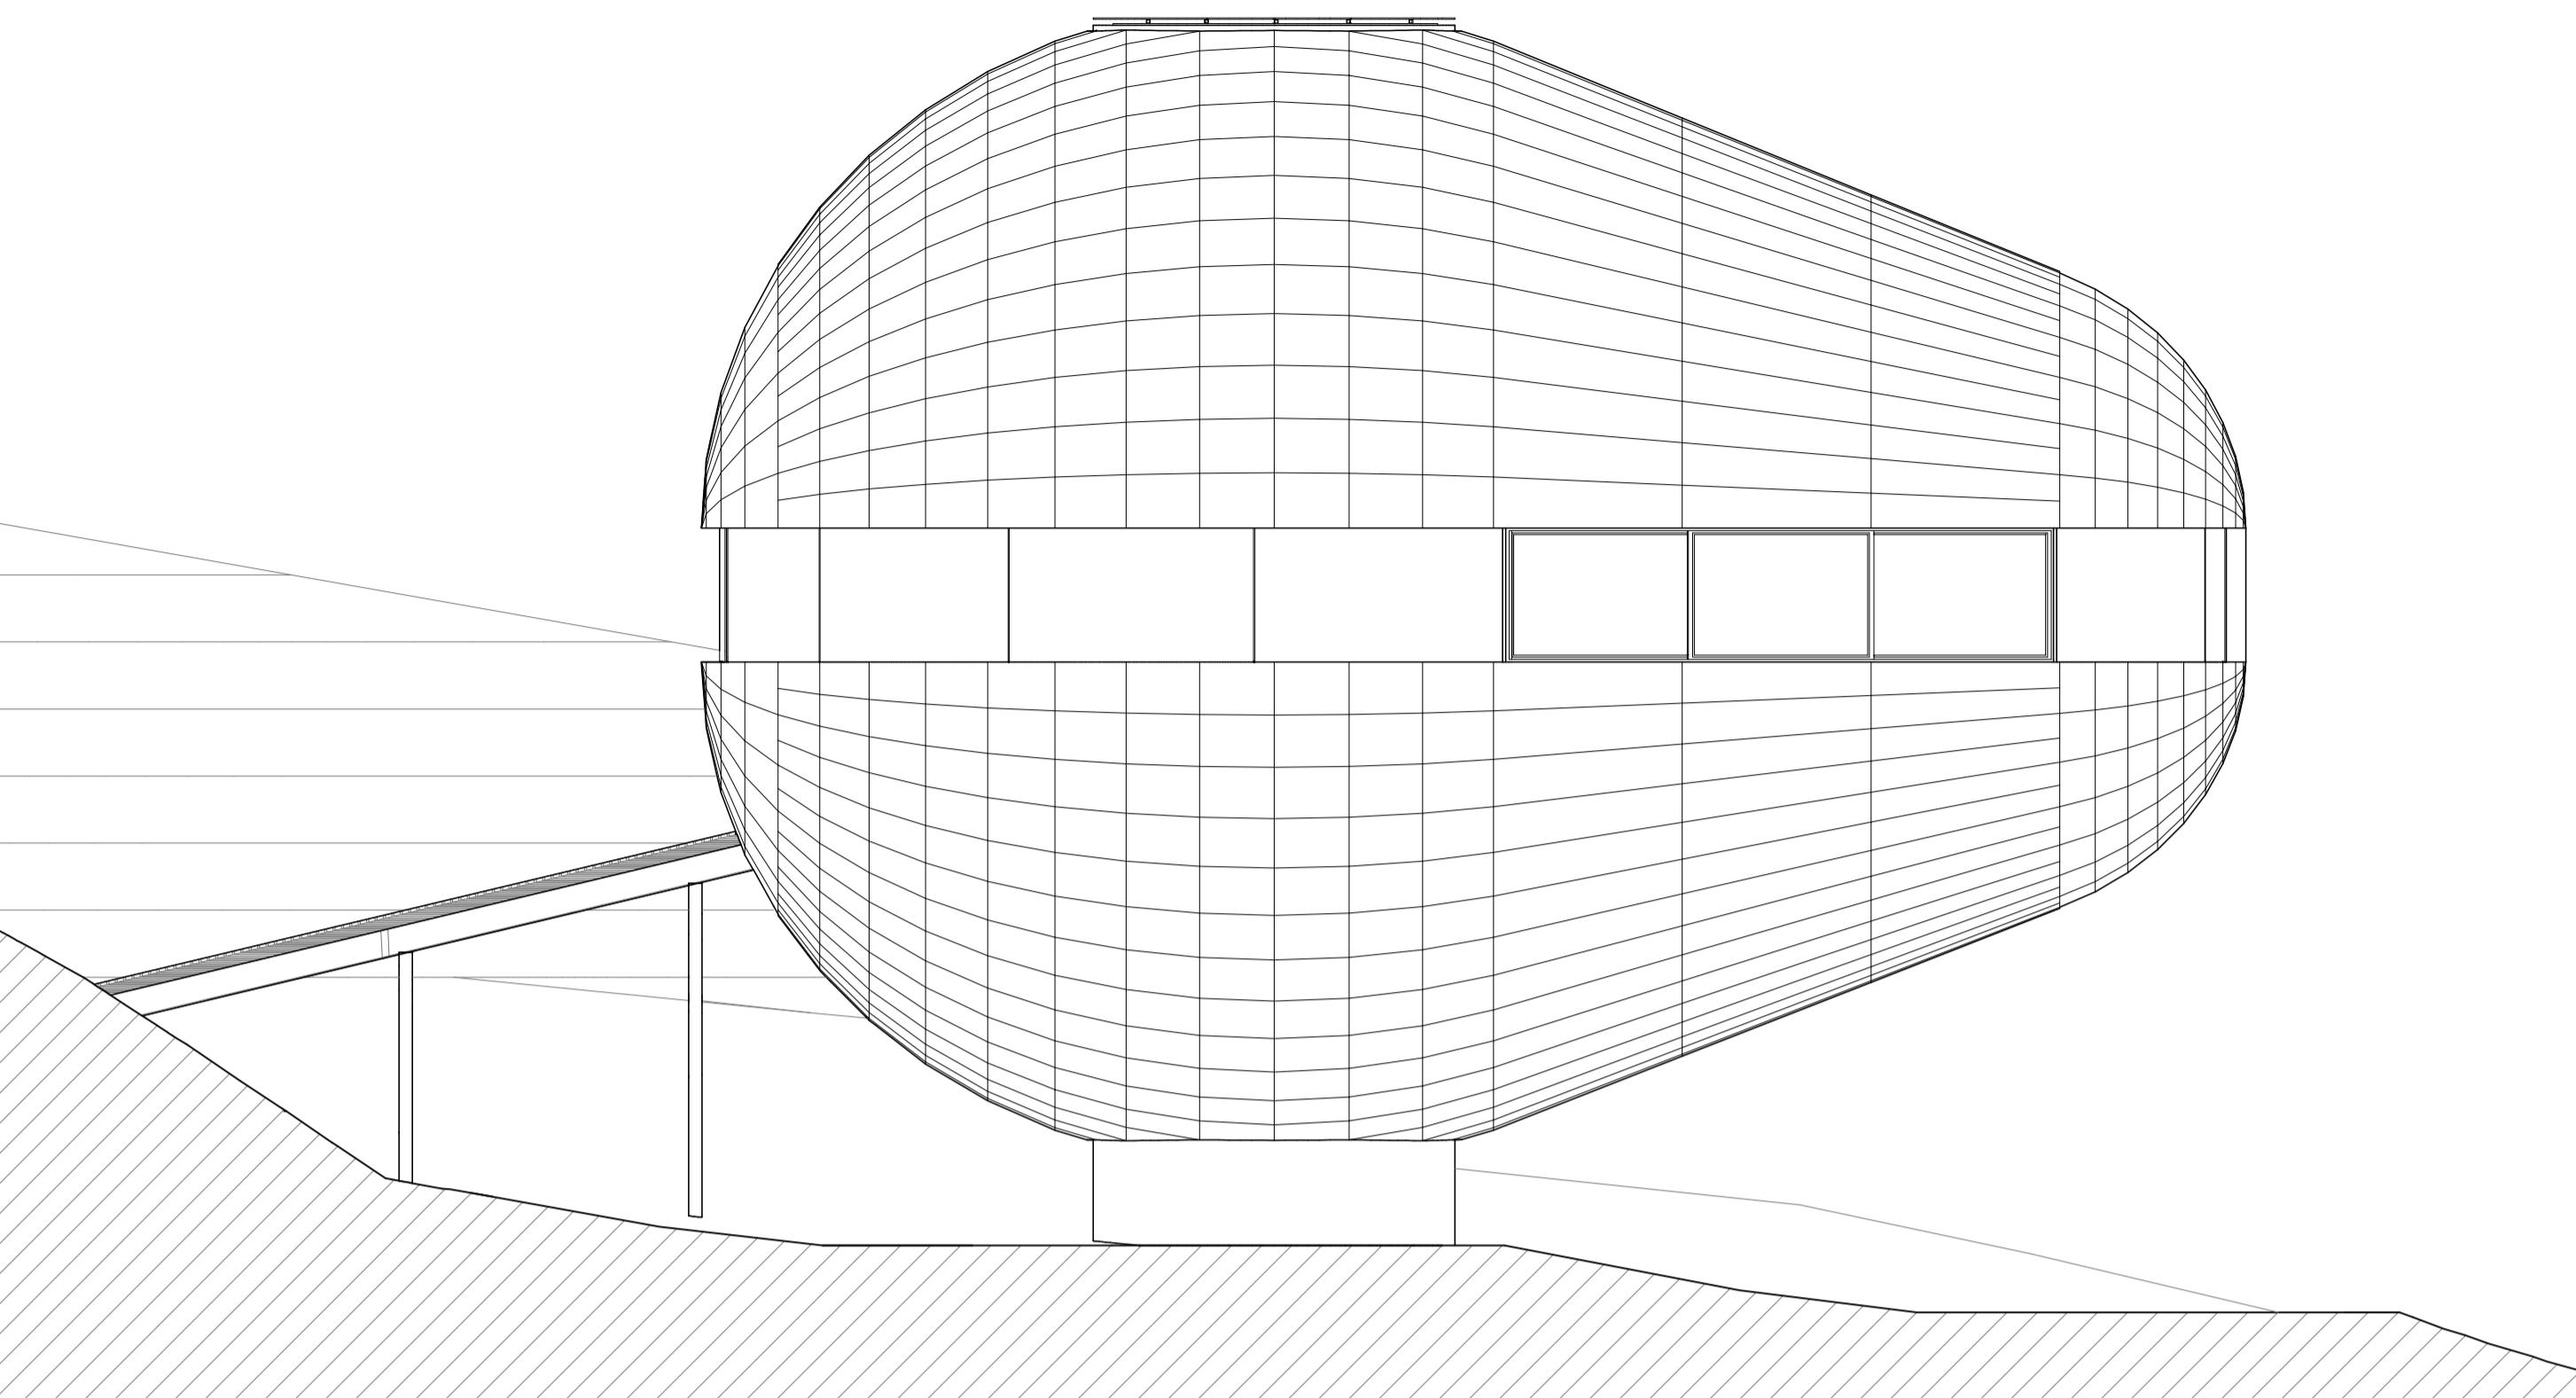


ELEVACIÓN SUR
esc. 1:50

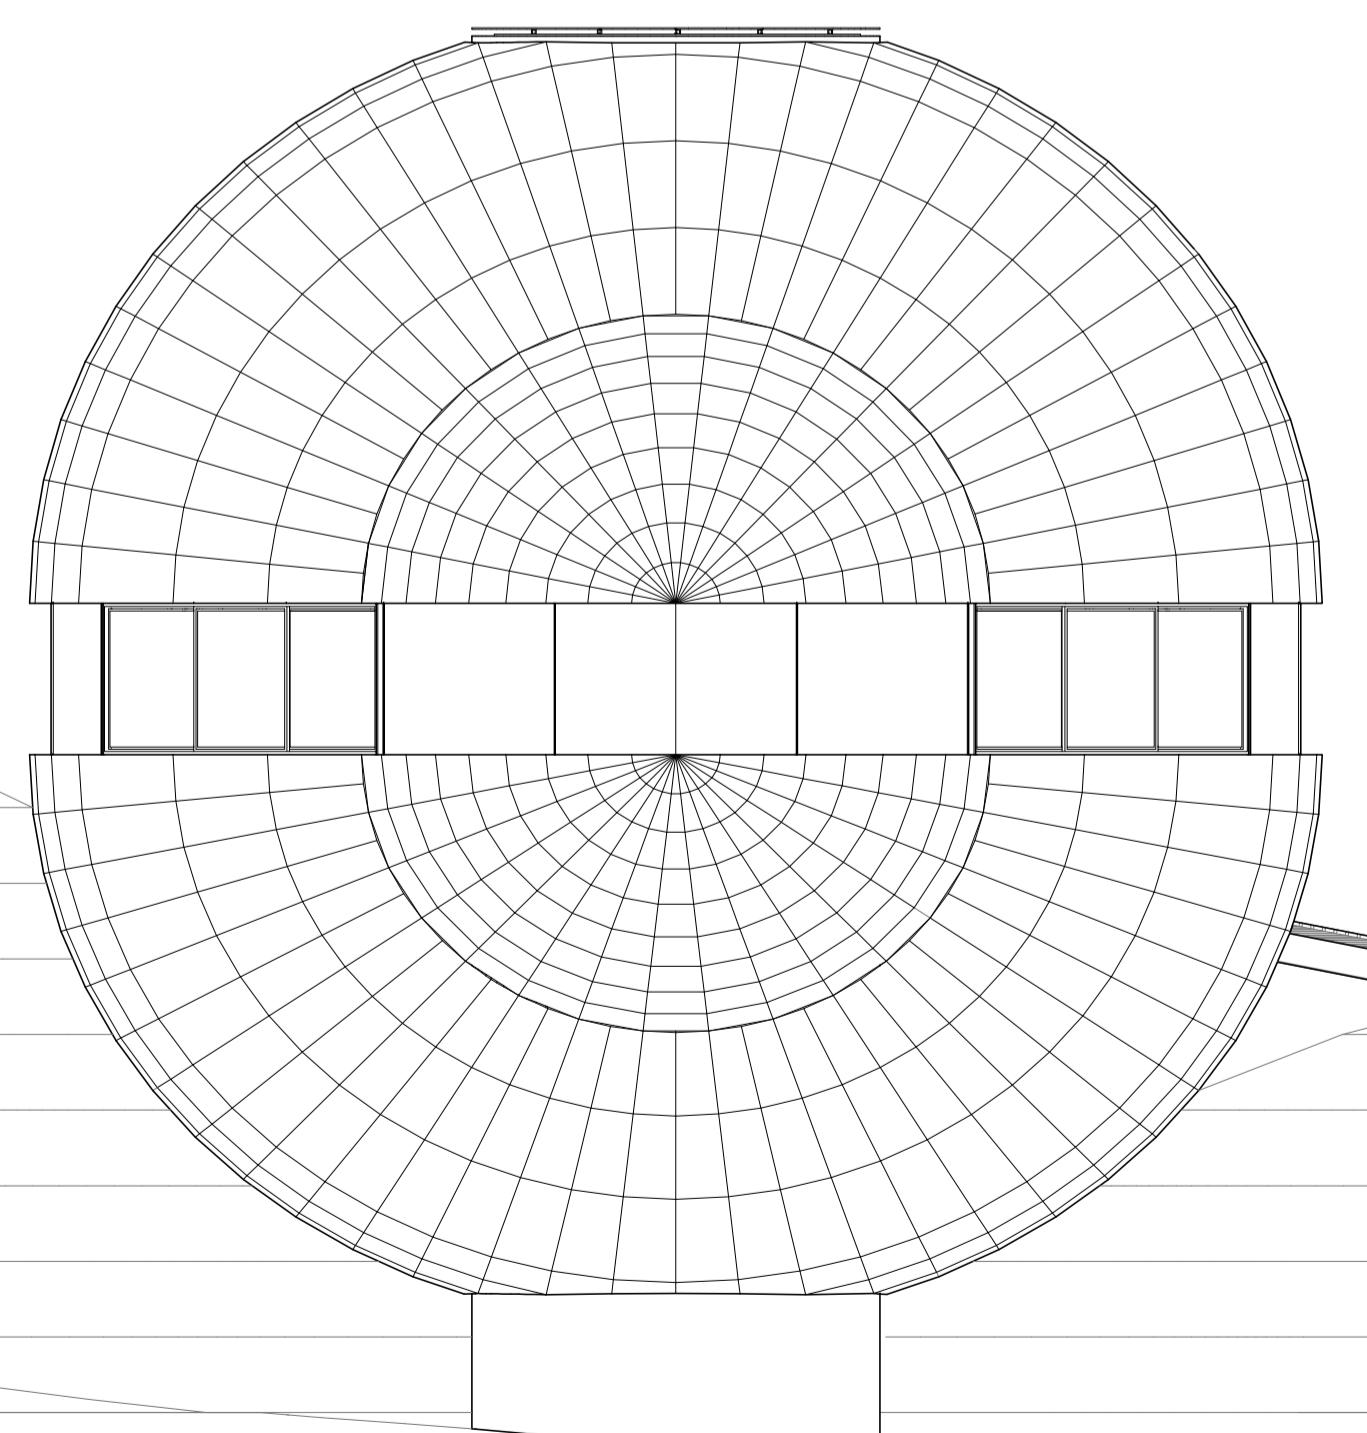

ELEVACIÓN PONIENTE
esc. 1:50

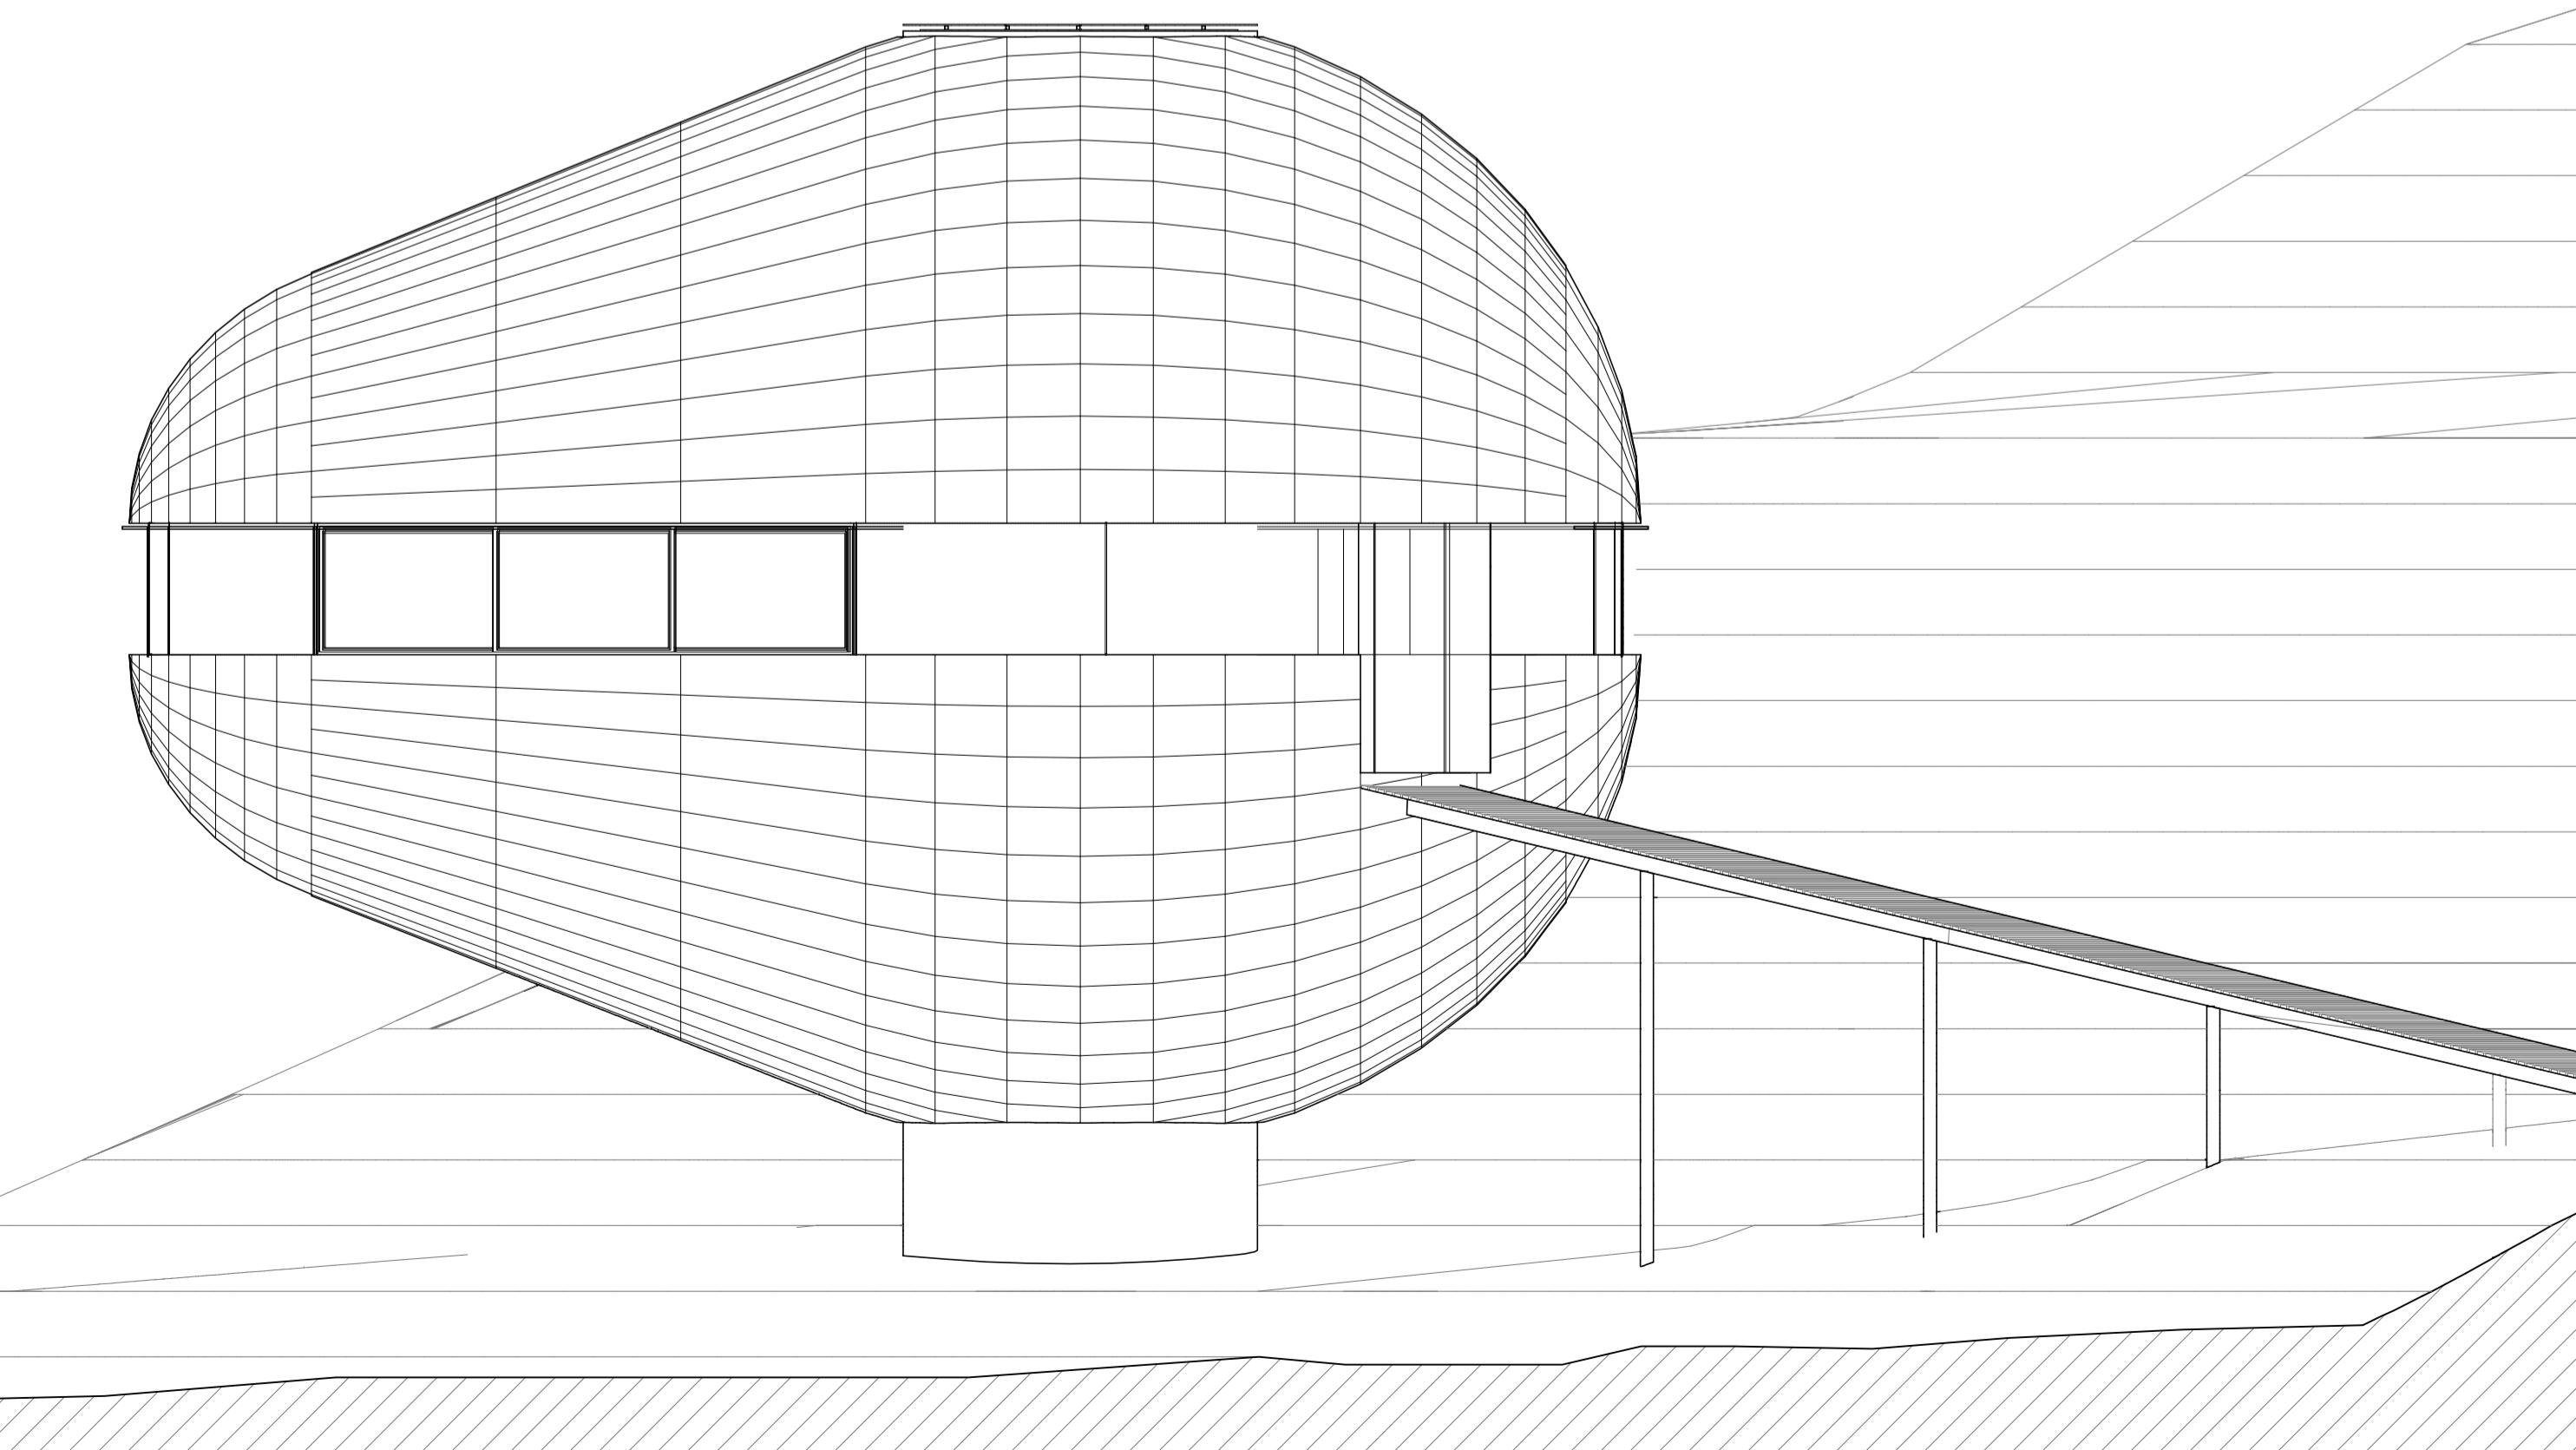


ELEVACIÓN NORTE
esc. 1:50

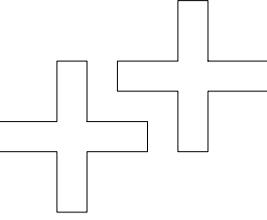

PROYECTO

Habitaculo
Palta Airbnb.

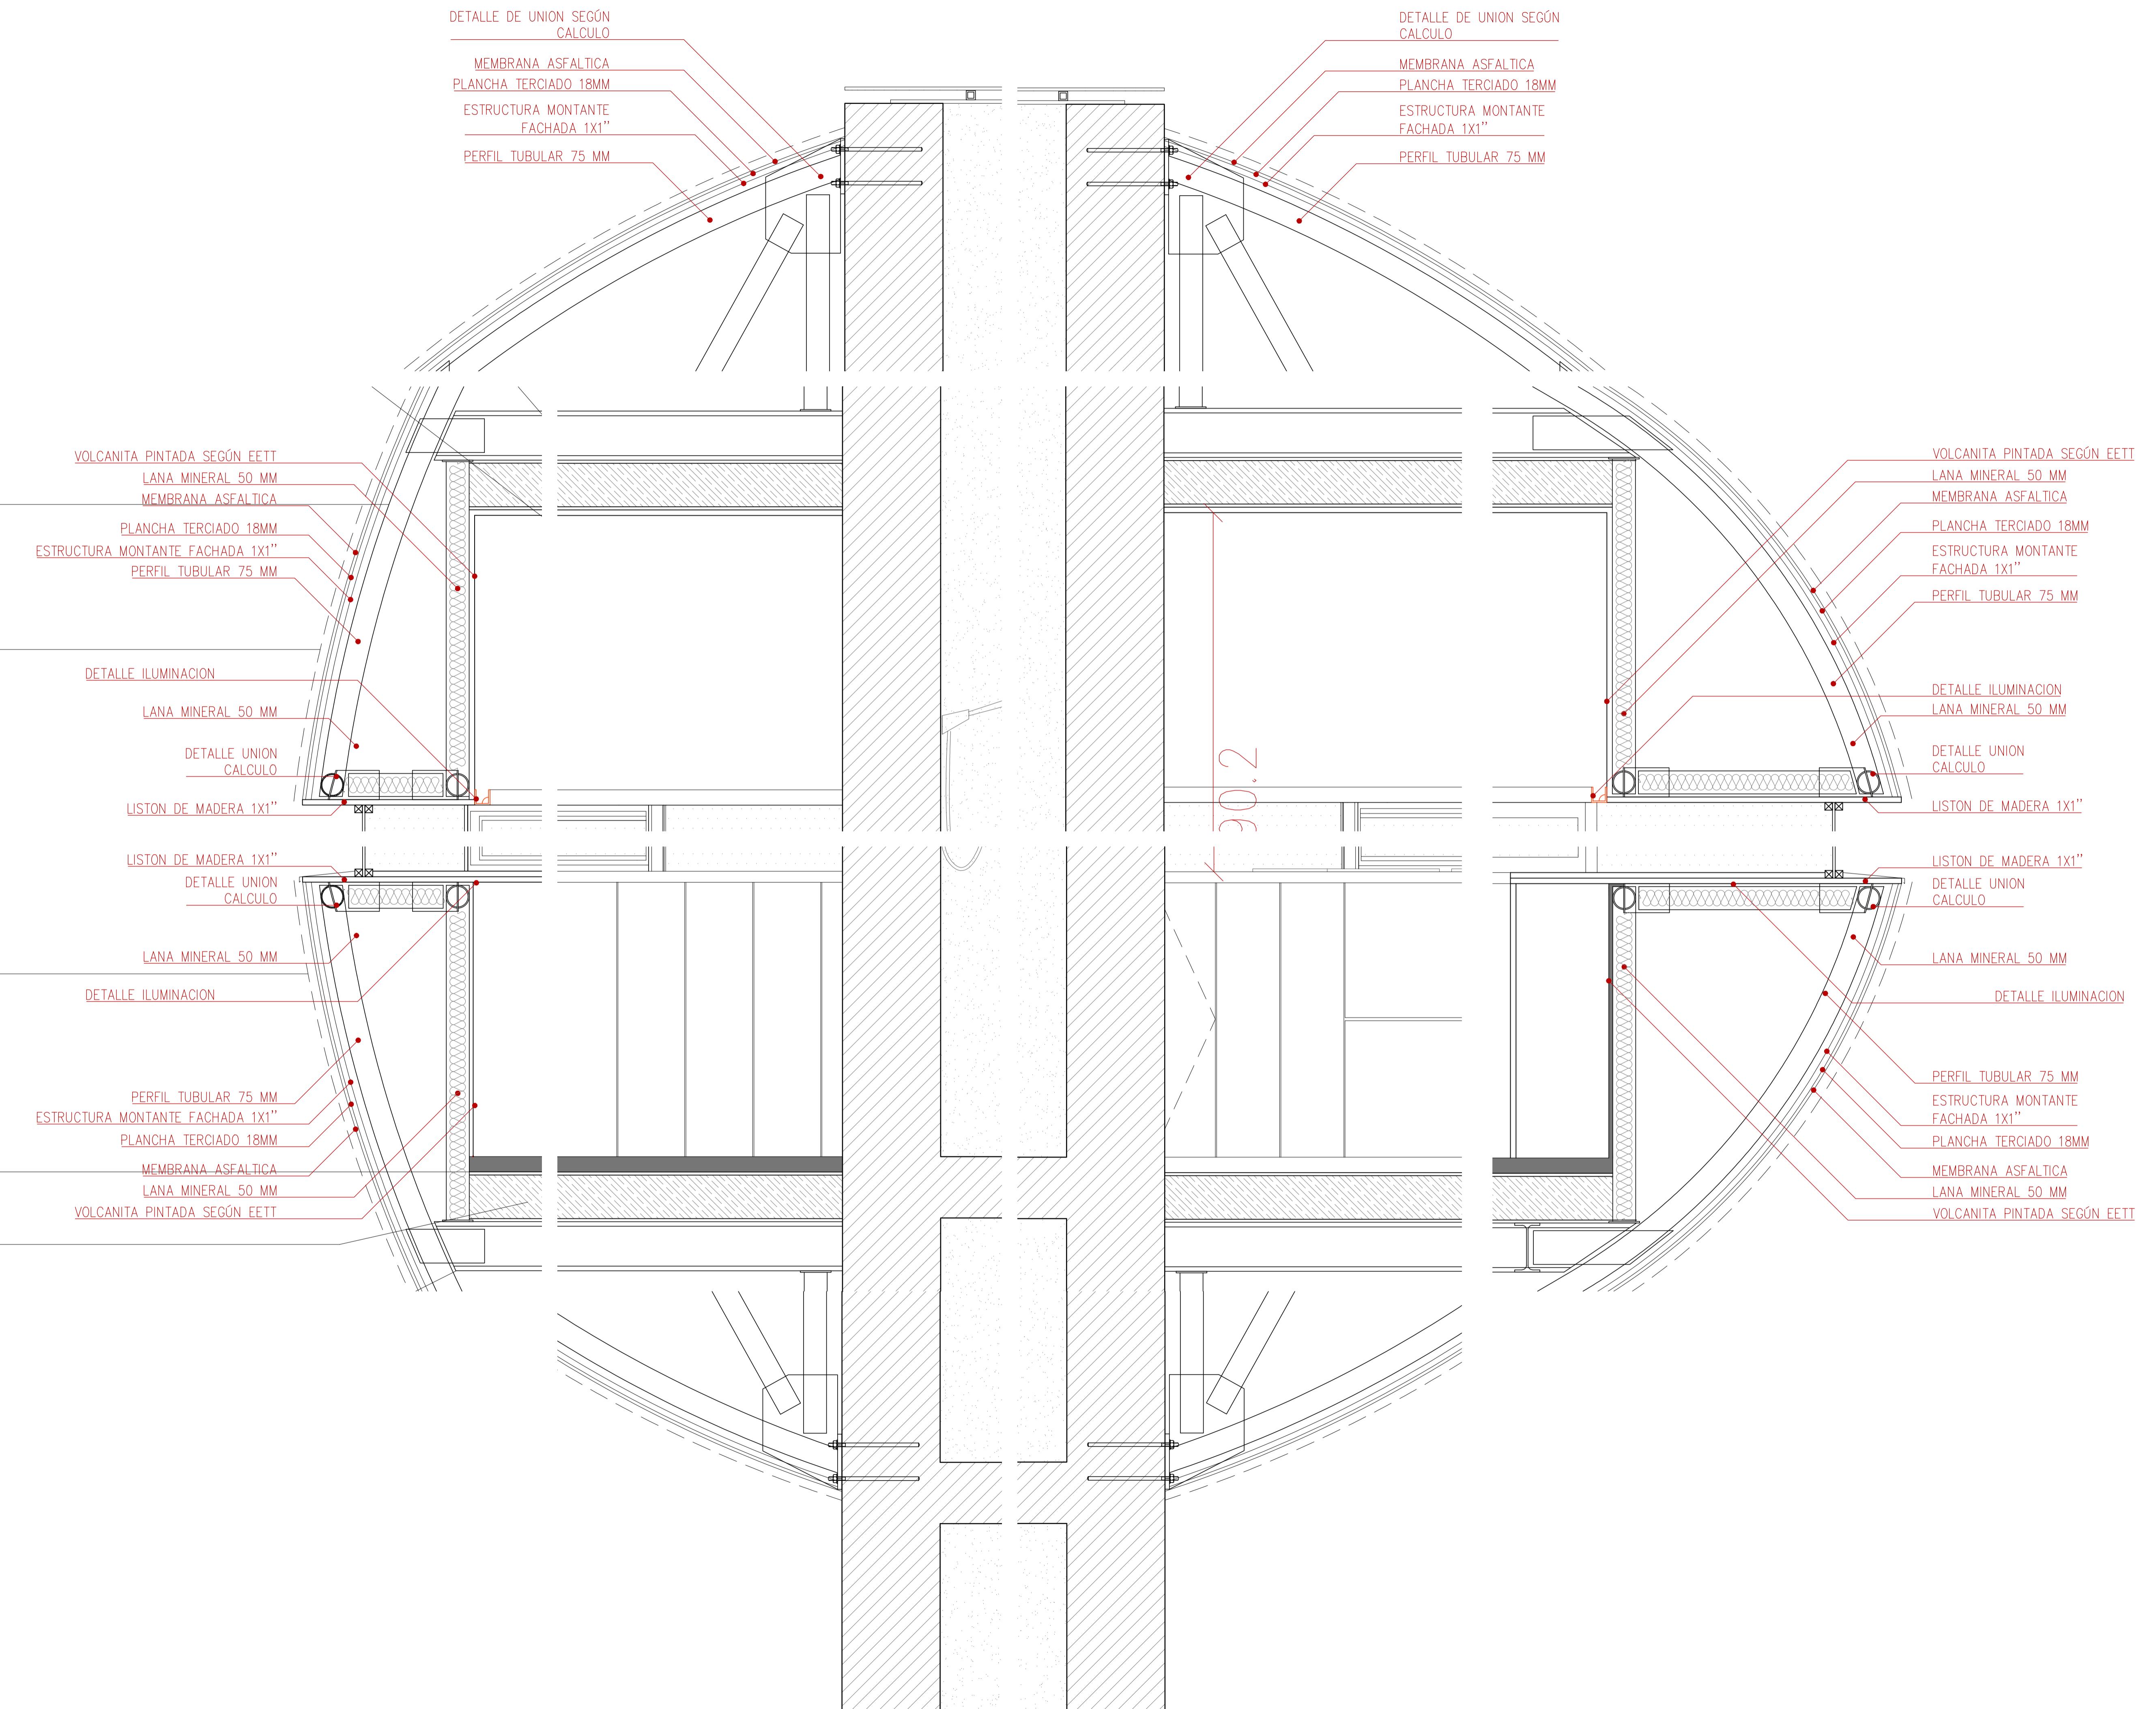

NOTAS

EDICIÓN

Entrega 01 Airbnb

MANDANTE

Ignacio Rios Michelsen
Rut:

ARQUITECTOS

MAS ES MAS
Arquitectos
Lucas Cerdá Ramoneda
19.078.130-5
Gabriel Oyarzún Casasus
16.742.060-1

DIBUJO

MAS ES MAS
Arquitectos

UBICACIÓN

Comuna de Hijuelas
Provincia de Quillota
Región de Valparaíso, Chile

Orientación




FECHA

2023 - 01 - 12












ESCALA

LÁMINA

1 : 50 ARQ_05

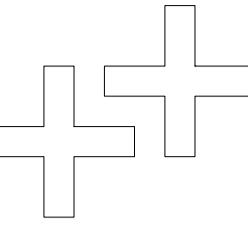

PROYECTO

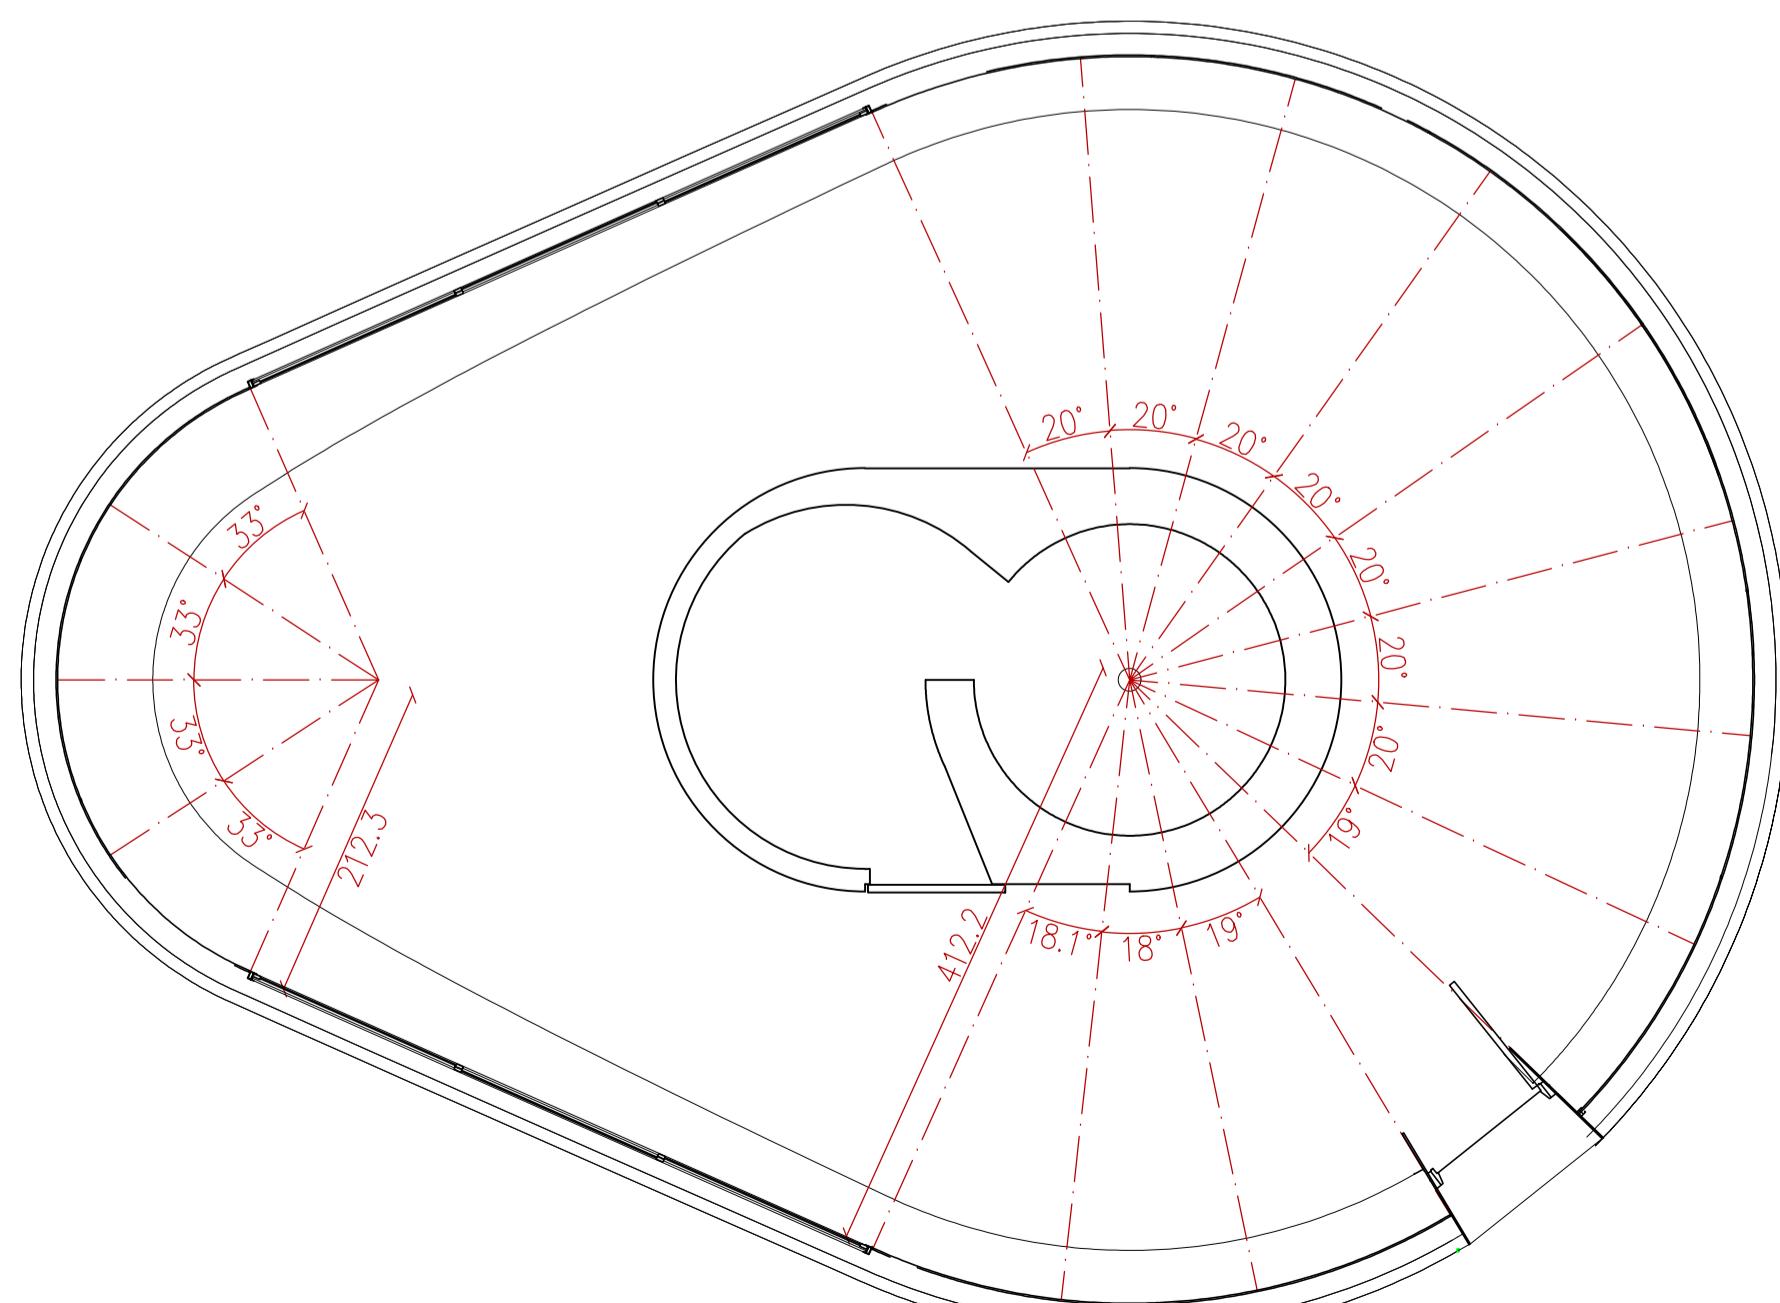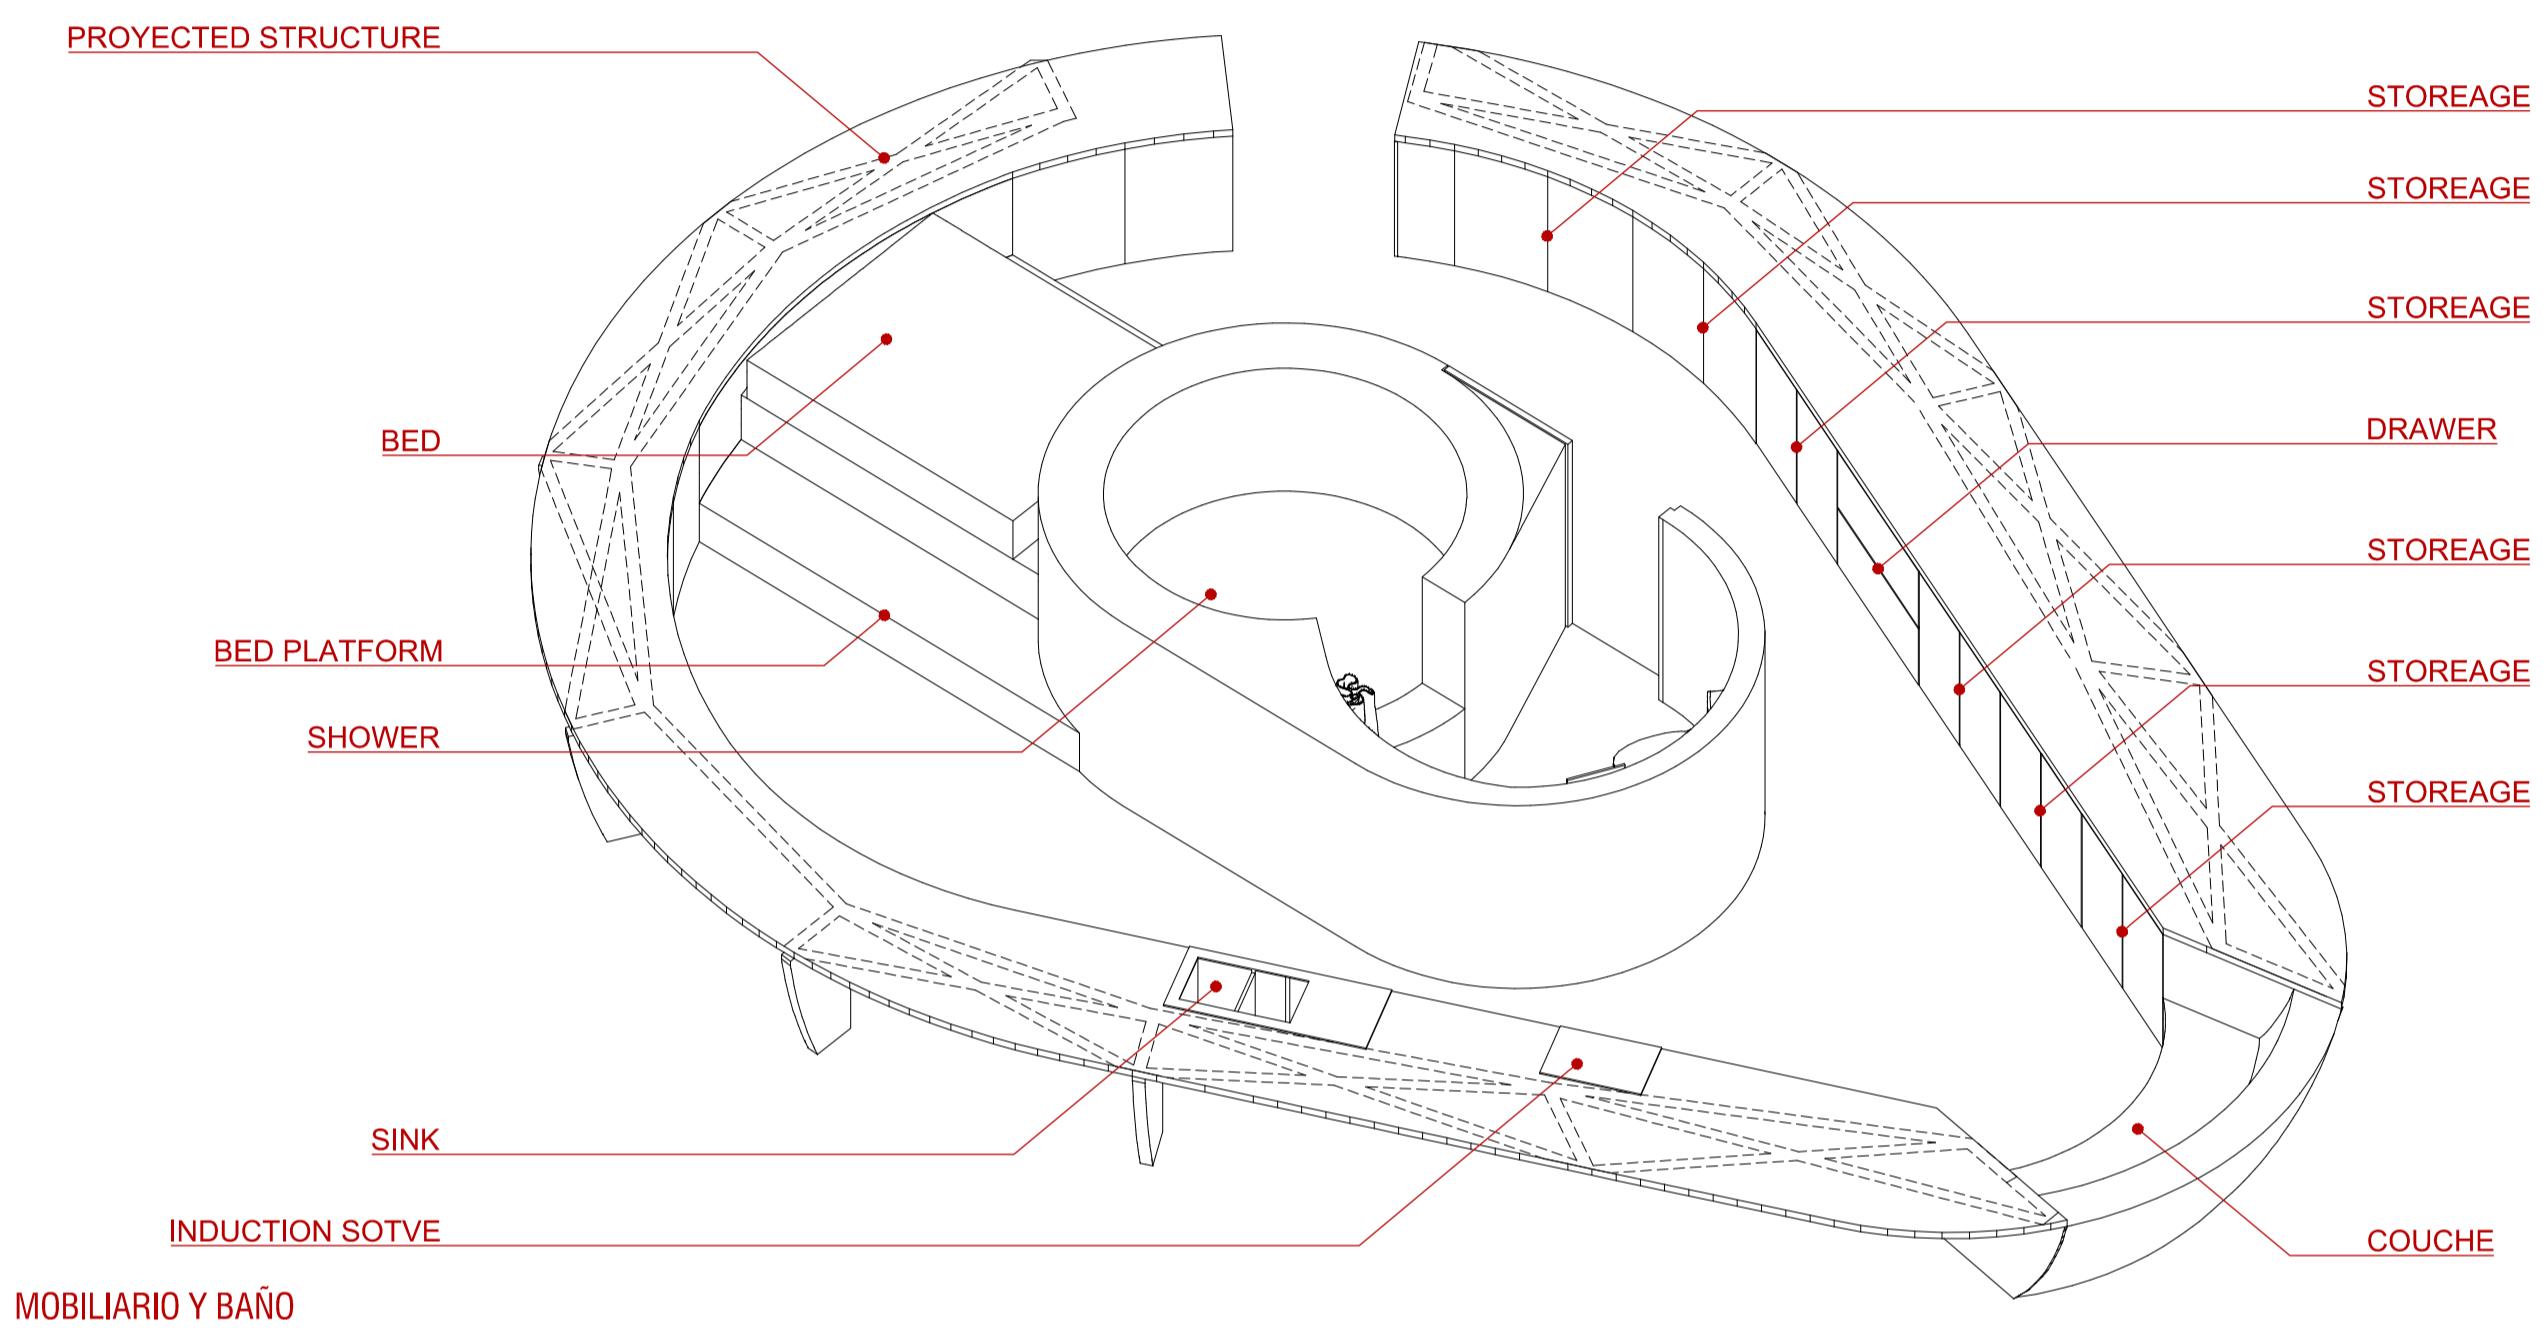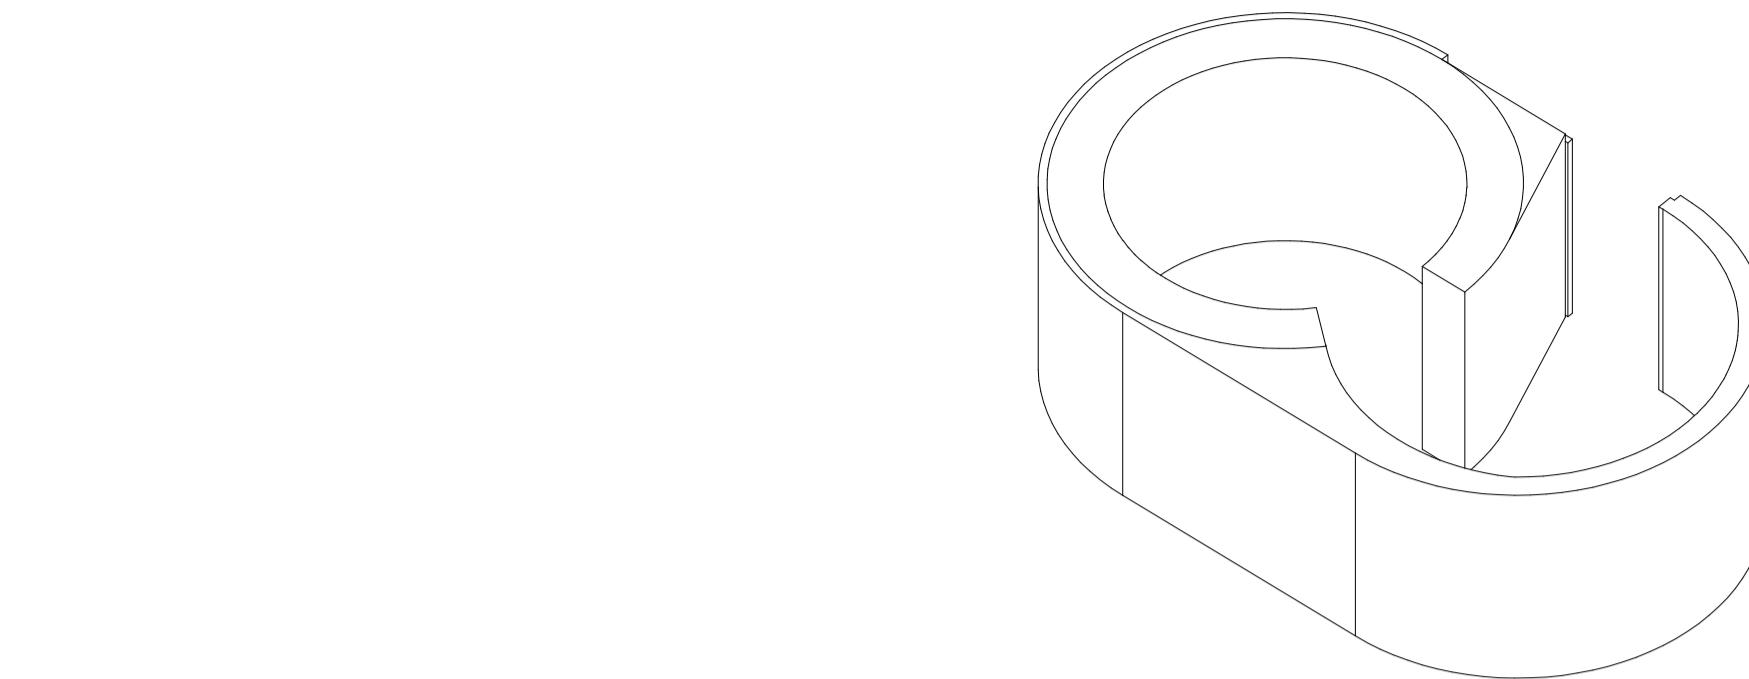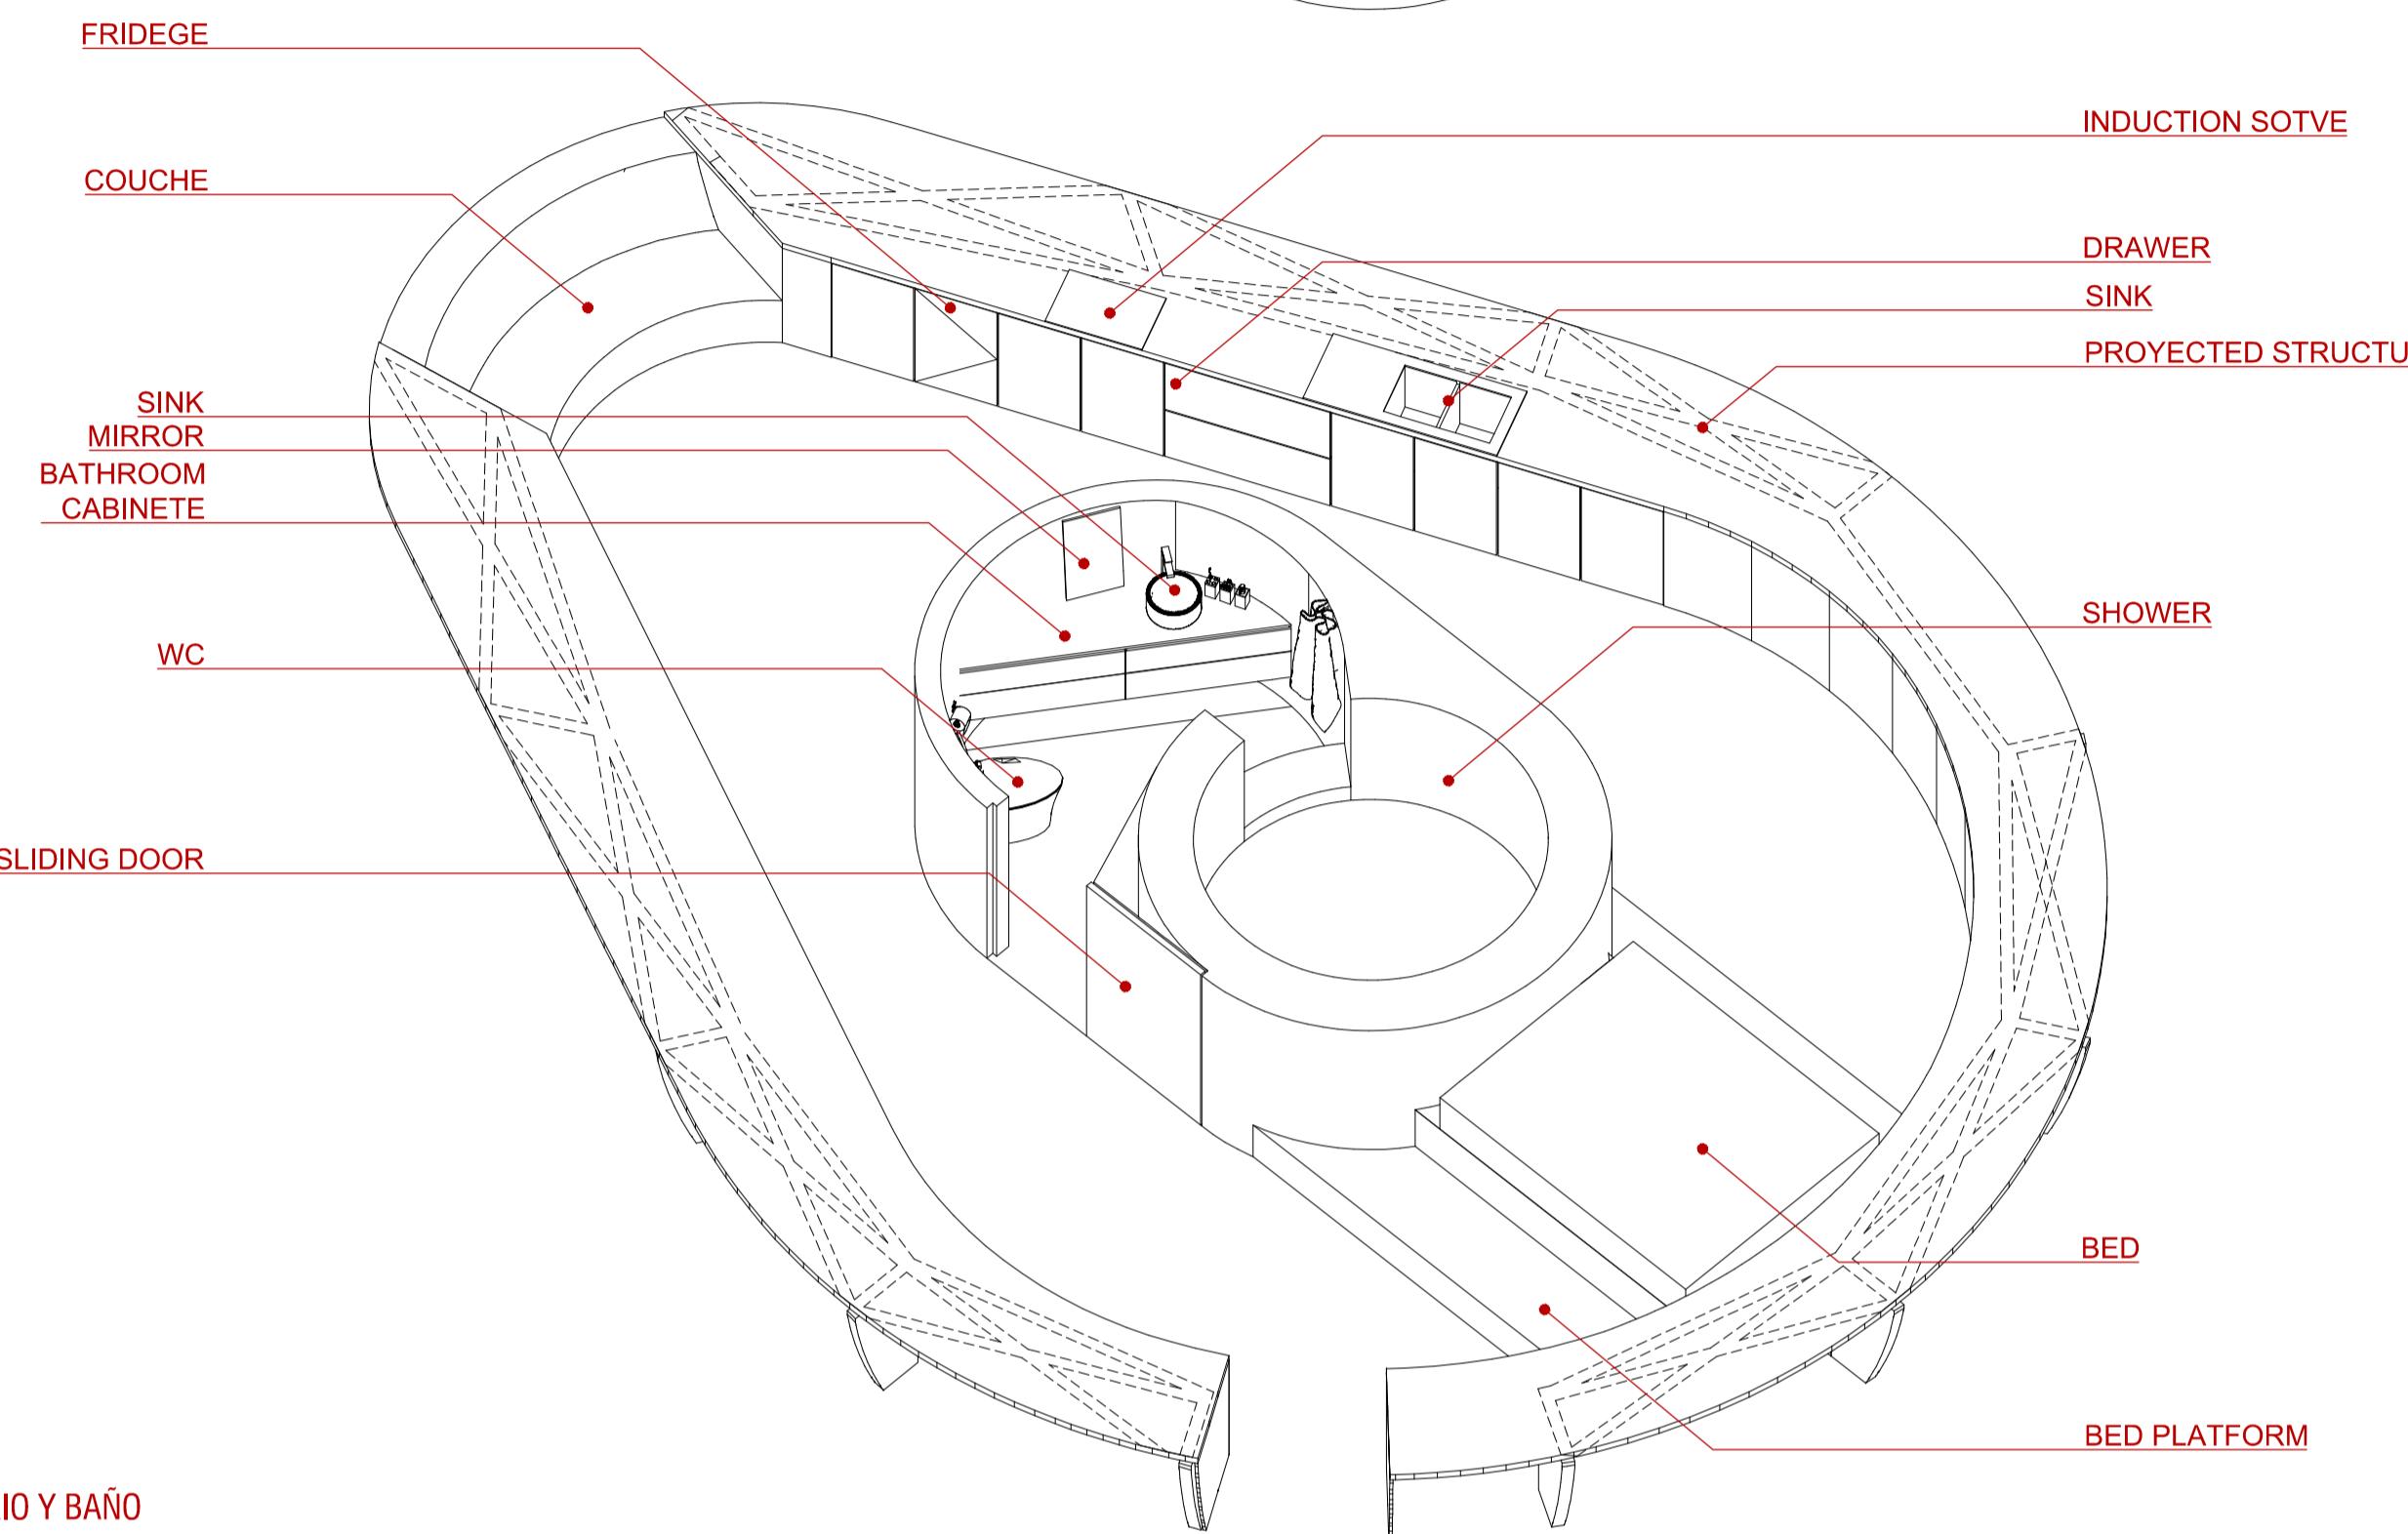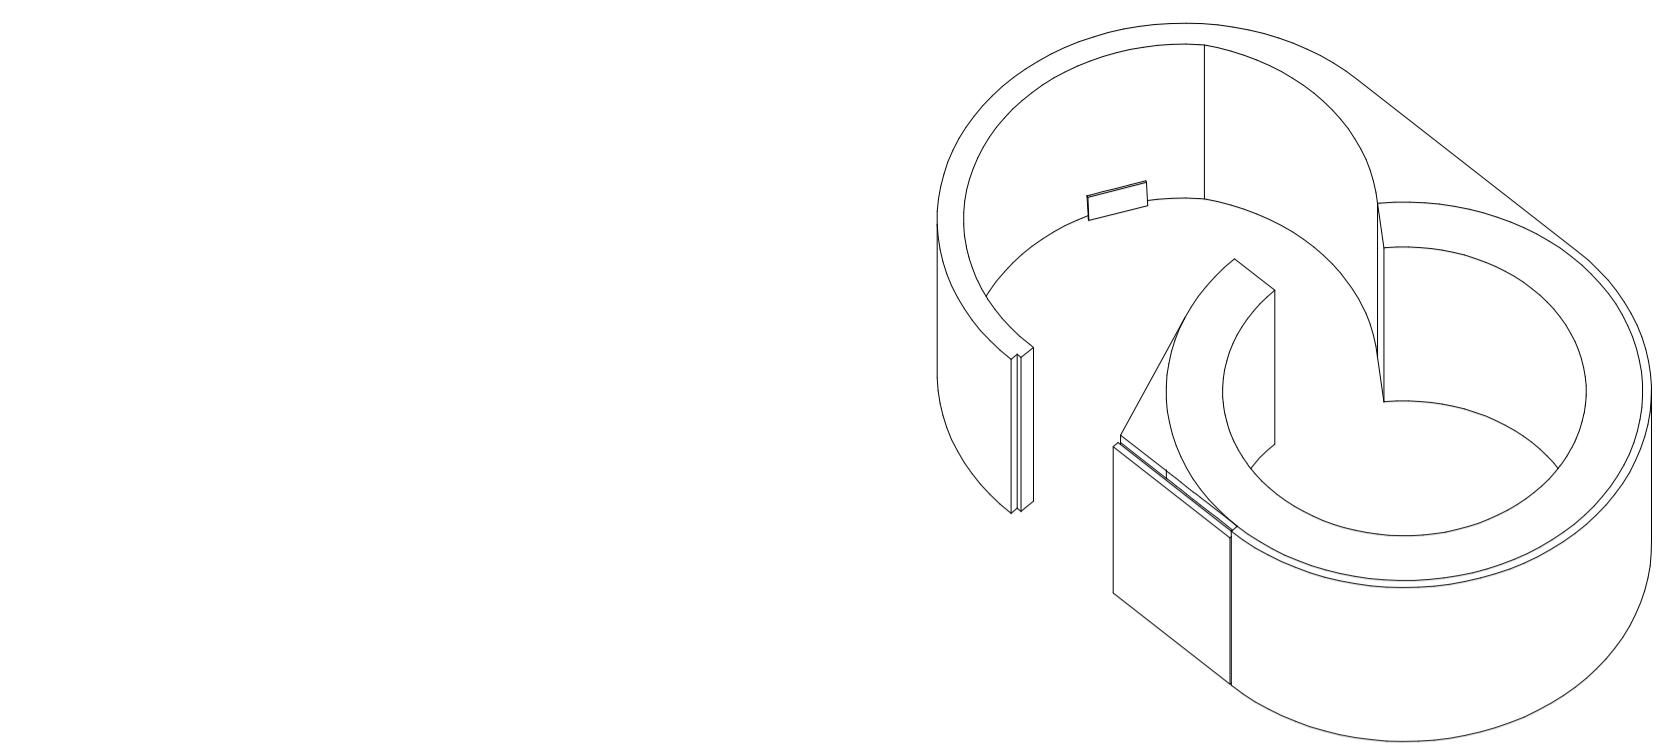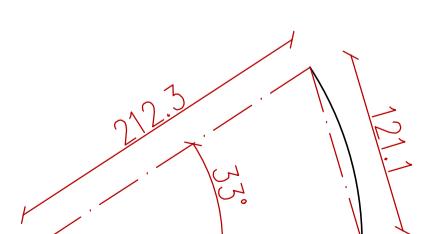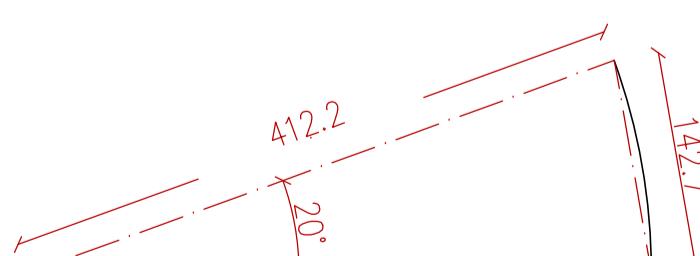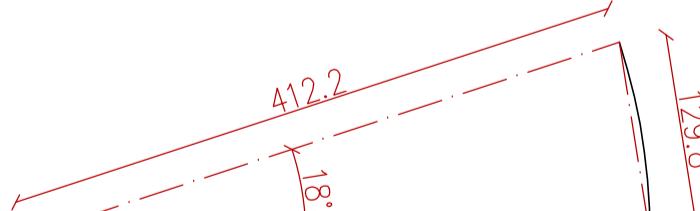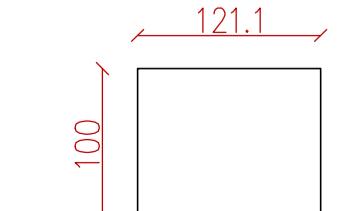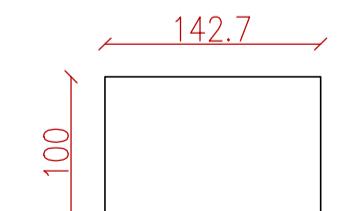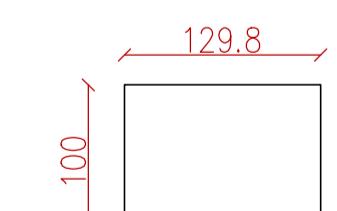**Habitaculo
Palta Airbnb.**DETALLE VENTANAS
esc. 1:50**Elevaciones Plantas****3 unidades****8 unidades****4 unidades**

NOTAS

EDICIÓN

Entrega 01 Airbnb

MANDANTE

Ignacio Ríos Michelsen
Rut:

ARQUITECTOS

MAS ES MAS
Arquitectos
Lucas Cerdá Ramoneda
19.078.130-5
Gabriel Oyarzún Casasus
16.742.060-1

DIBUJO

MAS ES MAS
Arquitectos

UBICACIÓN

Comuna de Hijuelas
Provincia de Quillota
Región de Valparaíso, Chile

Orientación




FECHA

2023 - 01 - 12

ESCALA

LÁMINA
1 : 50 ARQ_06

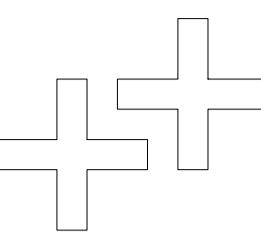

PROYECTO

Habitaculo Palta Airbnb.



NOTAS

EDICIÓN

Entrega 01 Airbnb

MANDANTE

Ignacio Ríos Michelsen
Rut:

ARQUITECTOS

MAS ES MAS
Arquitectos
Lucas Cerdá Ramoneda
19.078.130-5
Gabriel Oyarzún Casasus
16.742.060-1

DIBUJO

MAS ES MAS
Arquitectos

UBICACIÓN

Comuna de Hijuelas
Provincia de Ñuble
Región de Valparaíso, Chile

Orientación



FECHA


2023 - 01 - 12

ESCALA

LÁMINA

1 : 50

ARQ_08

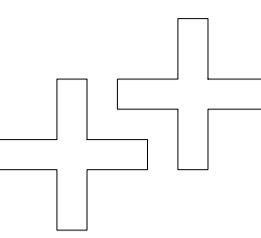

PROYECTO

Habitaculo Palta Airbnb.

NOTAS

EDICIÓN

Entrega 01 Airbnb

MANDANTE

Ignacio Ríos Michelsen
Rut:

ARQUITECTOS

MAS ES MAS
Arquitectos
Lucas Cerdá Ramoneda
19.078.130-5
Gabriel Oyarzún Cassasus
16.742.060-1

DIBUJO

MAS ES MAS
Arquitectos

UBICACIÓN

Comuna de Hijuelas
Provincia de Quillota
Región de Valparaíso, Chile

Orientación



FECHA

2023 - 01 - 12


ESCALA

LÁMINA

1 : 50

ARQ_09



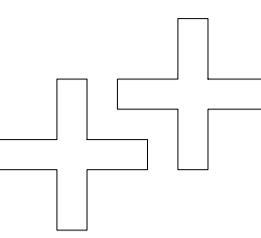

PROYECTO

**Habitaculo
Palta Airbnb.**

NOTAS

EDICIÓN

Entrega 01 Airbnb

MANDANTE

Ignacio Ríos Michelseth
Rut:

ARQUITECTOS

MAS ES MAS
Arquitectos
Lucas Cerdá Ramoneda
19.078.130-5
Gabriel Oyarzún Casasus
16.742.060-1


DIBUJO

MAS ES MAS
Arquitectos

UBICACIÓN

Comuna de Hijuelas
Provincia de Quillota
Región de Valparaíso, Chile

Orientación

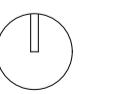

FECHA

2023 - 01 - 12


ESCALA

1 : 50

LÁMINA

ARQ_10



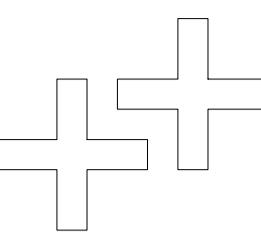

PROYECTO

Habitaculo Palta Airbnb.



NOTAS

EDICIÓN

Entrega 01 Airbnb

MANDANTE

Ignacio Ríos Michelseth
Rut:

ARQUITECTOS

MAS ES MAS
Arquitectos
Lucas Cerdá Ramoneda
19.078.130-5
Gabriel Oyarzún Cassasus
16.742.060-1


DIBUJO

MAS ES MAS
Arquitectos

UBICACIÓN

Comuna de Hijuelas
Provincia de Quillota
Región de Valparaíso, Chile

Orientación

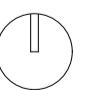

FECHA


2023 - 01 - 12

ESCALA

LÁMINA

1 : 50

ARQ_11

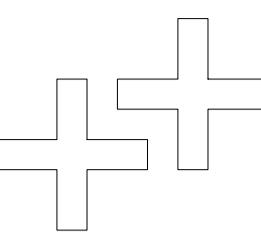

PROYECTO

Habitaculo
Palta Airbnb.

NOTAS

EDICIÓN

Entrega 01 Airbnb

MANDANTE

Ignacio Ríos Michelseth
Rut:

ARQUITECTOS

MAS ES MAS
Arquitectos
Lucas Cerdá Ramoneda
19.078.130-5
Gabriel Oyarzún Cassasus
16.742.060-1


DIBUJO

MAS ES MAS
Arquitectos

UBICACIÓN

Comuna de Hijuelas
Provincia de Quillota
Región de Valparaíso, Chile

Orientación

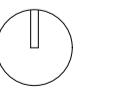

FECHA

2023 - 01 - 12

ESCALA



1 : 50

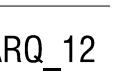


LÁMINA
ARQ_12

